


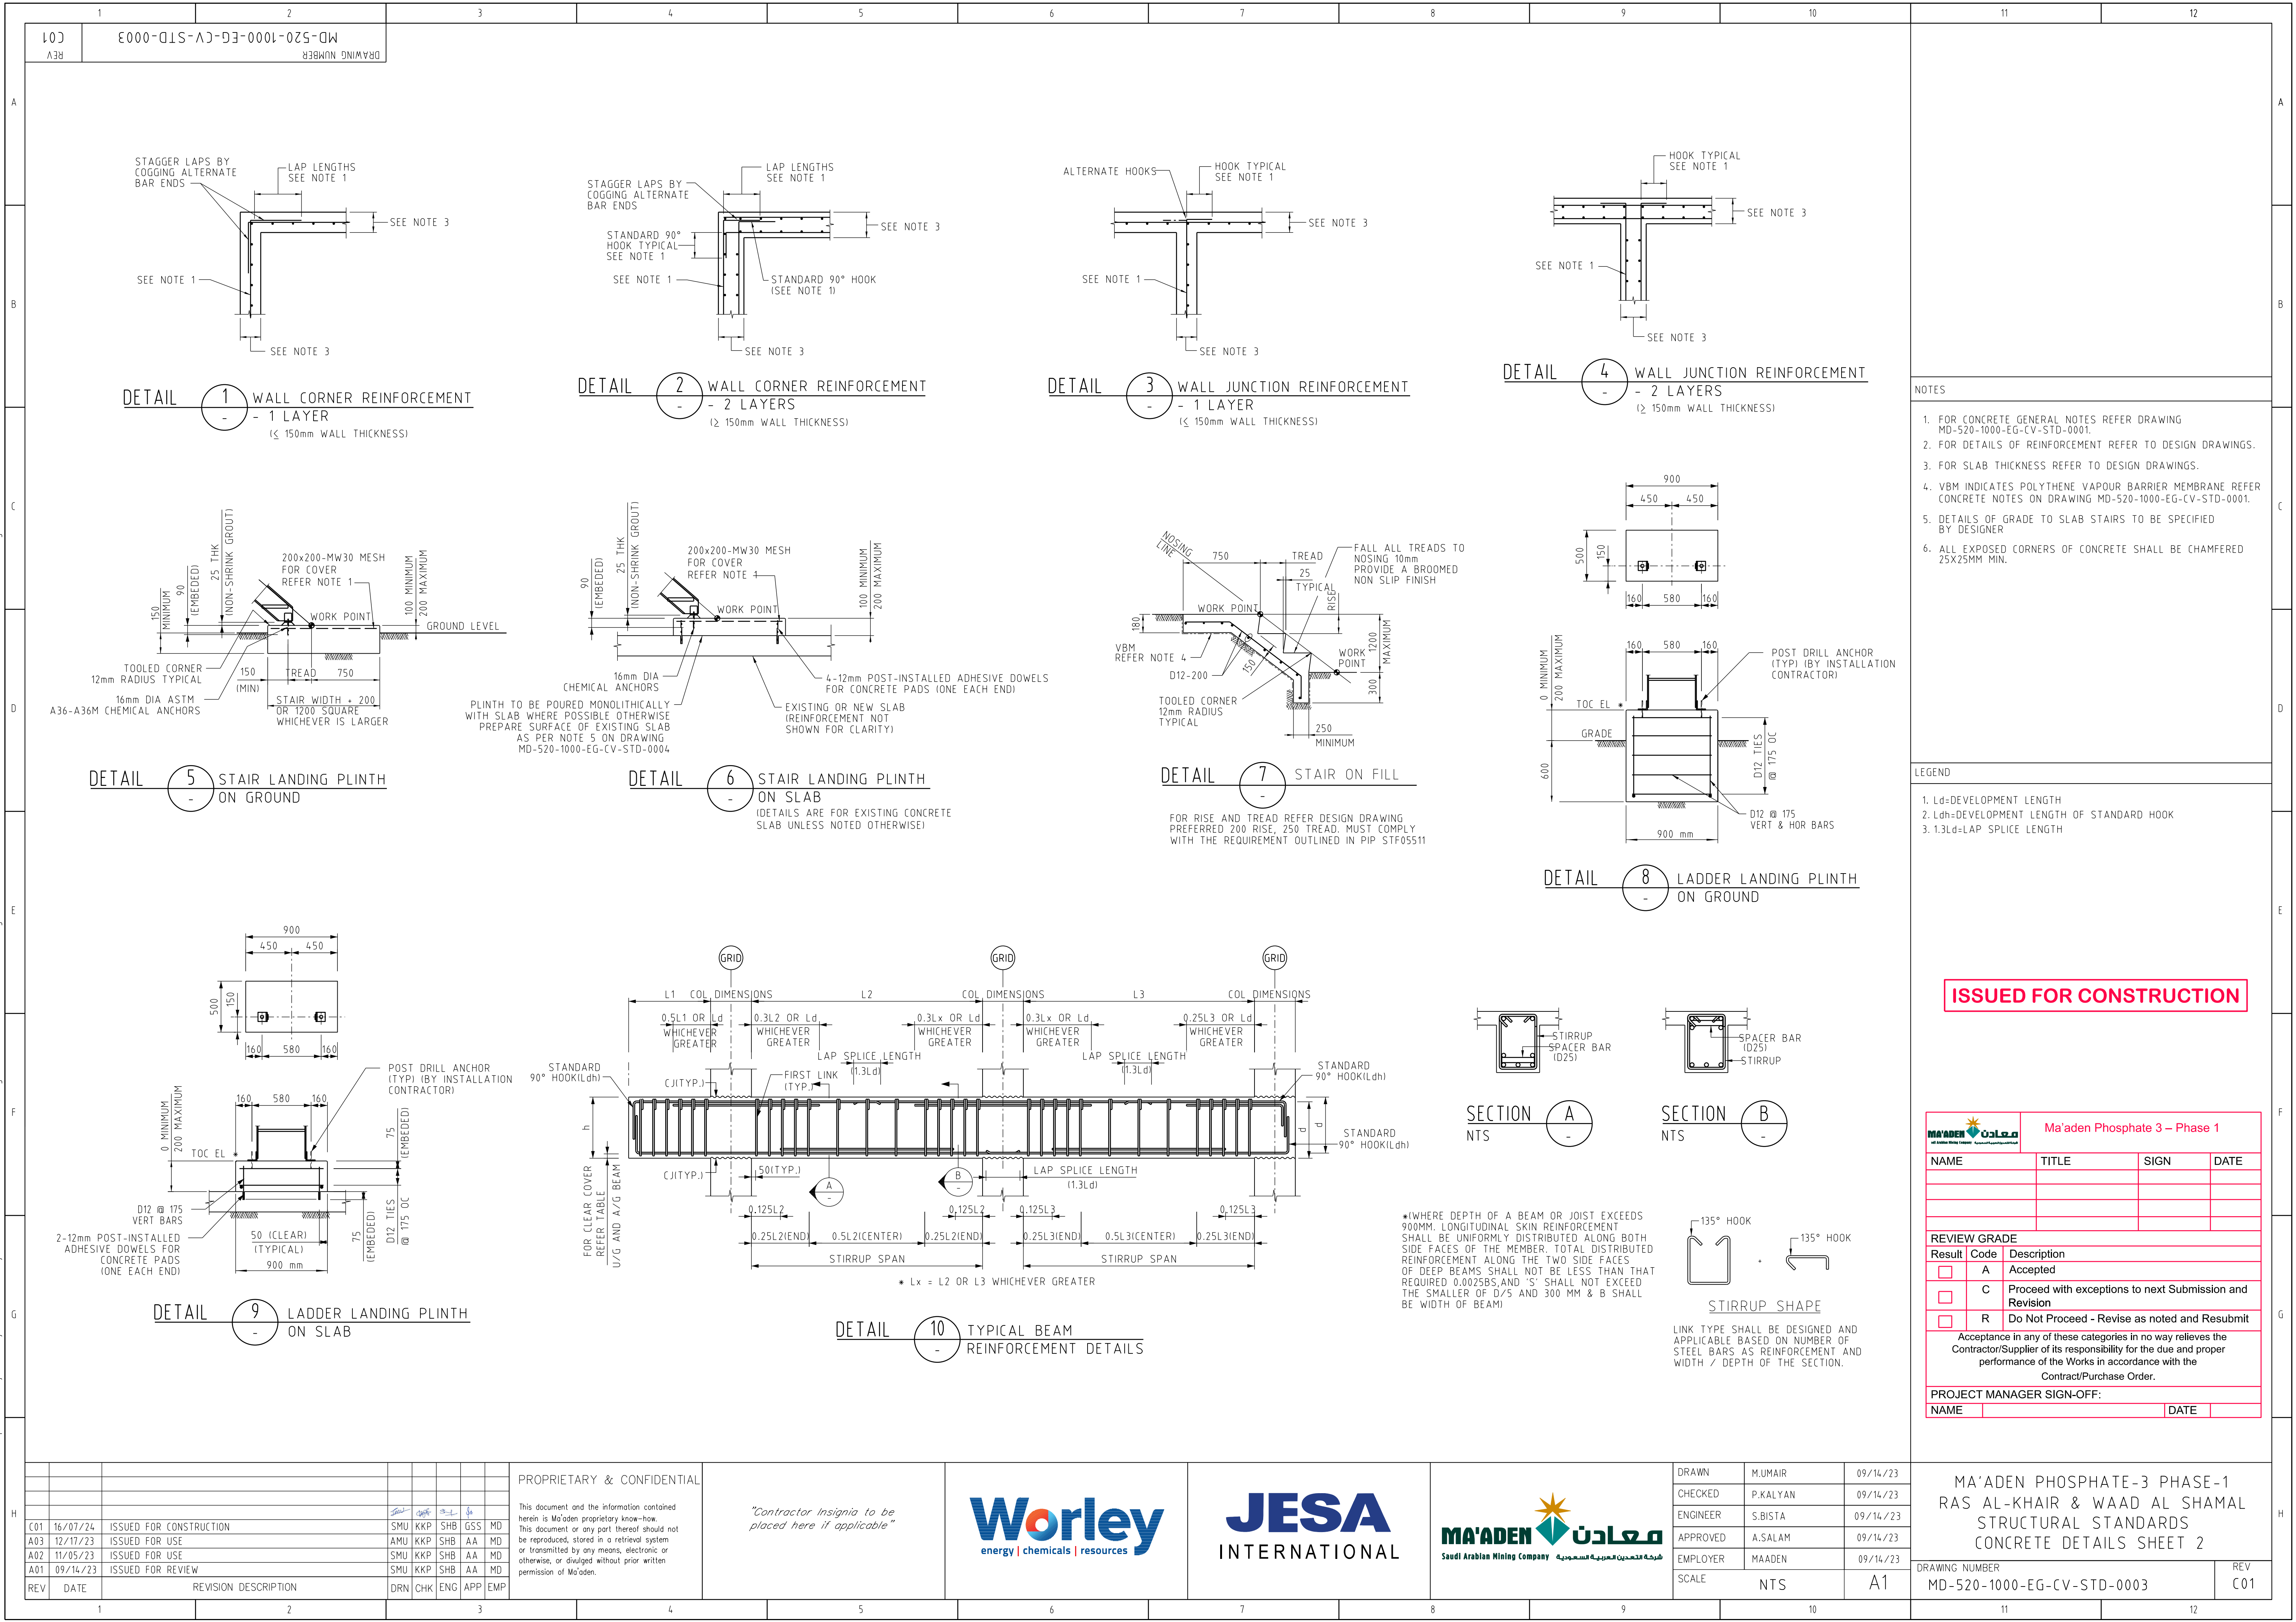

PROPRIETARY & CONFIDENTIAL

This document and the information contained herein is Ma'aden proprietary know-how. This document or any part thereof should not be reproduced, stored in a retrieval system or transmitted by any means, electronic or otherwise, or divulged without prior written permission of Ma'aden.

"Contractor Insignia to be placed here if applicable"

