
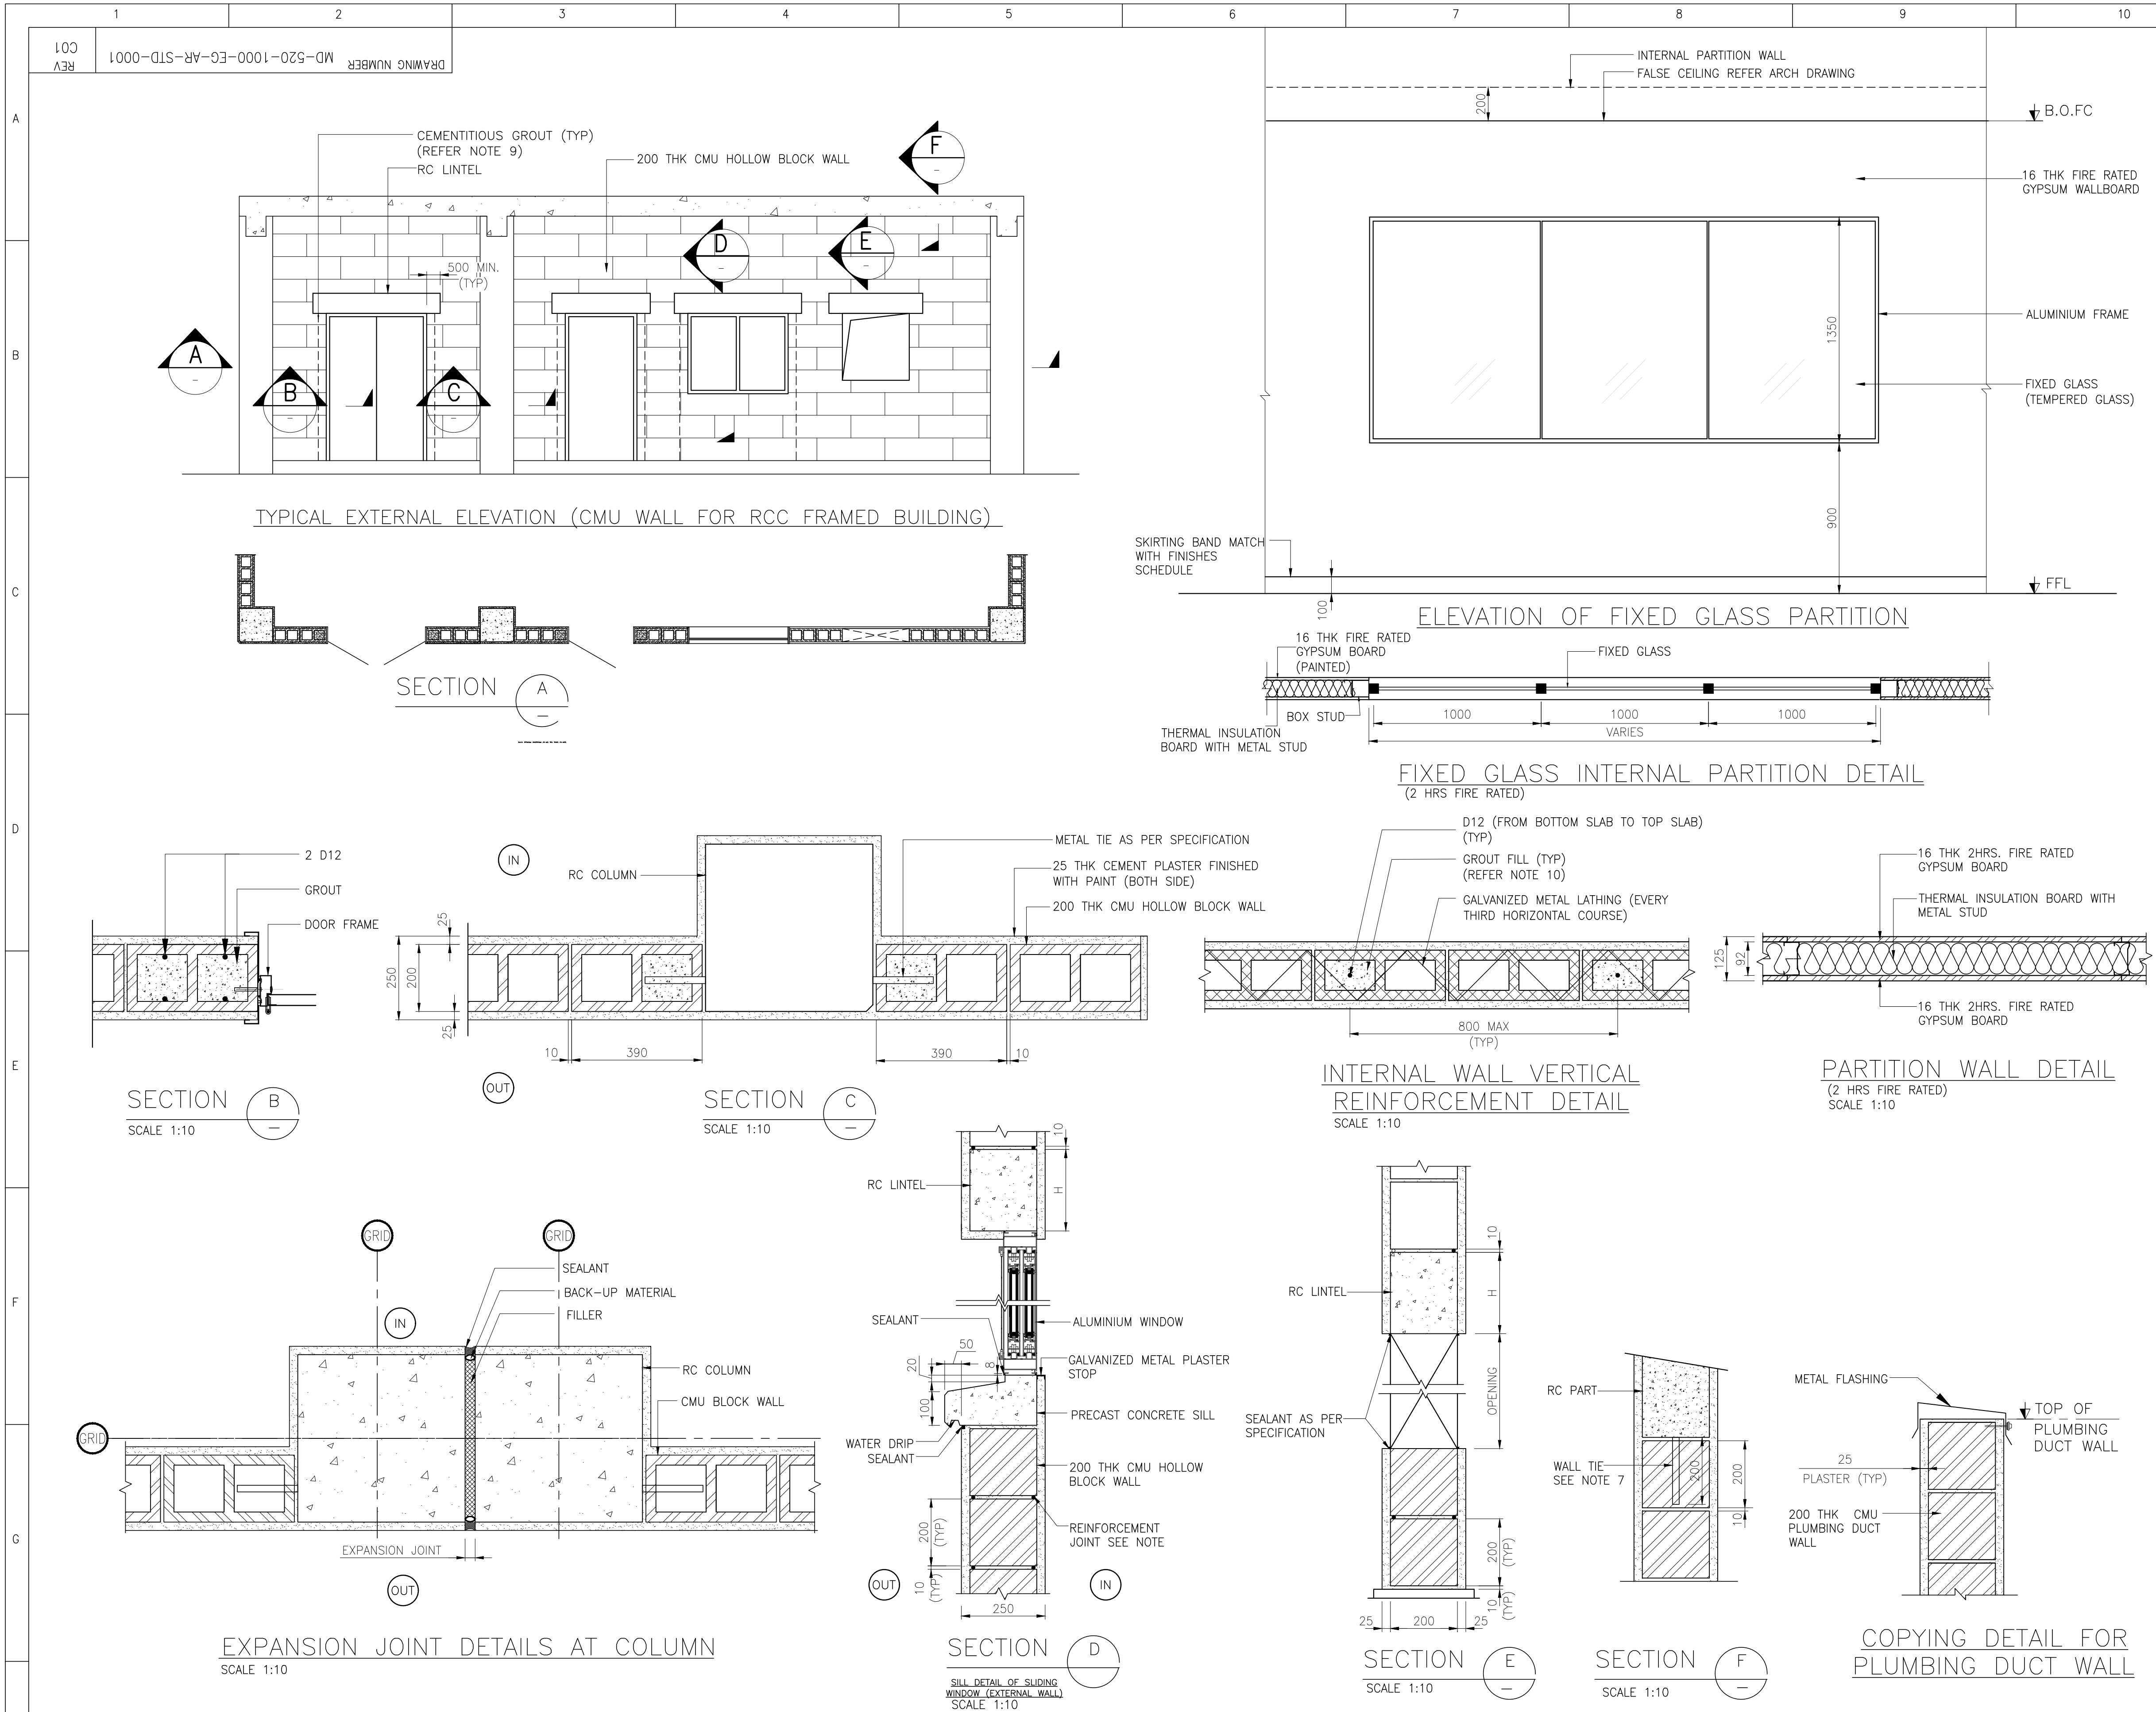


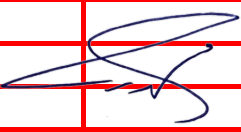

- GENERAL NOTES:**
1. ALL TYPICAL DETAILS SHALL BE READ IN CONJUNCTION WITH ARCHITECTURAL DRAWINGS.
 2. MEASURE IN MILLIMETRE, LEVELS IN METRE.
 3. HOLLOW CONCRETE BLOCK:
FACE DIMENSIONS 390 x 200 x 200 MM
MORTAR SHALL CONFIRM ASTM C270.
 4. REINFORCED CONCRETE STUDS SHALL BE PROVIDED IF WALL AREA EXCEEDS 20 SQ.M.
CONCRETE STUDS SHALL BE FIXED HORIZONTALLY AT BOTTOM AND TOP.
 5. REINFORCED JOINTS EACH CONSISTING OF 2 R12 GALVANIZED REBARS HAVE TO BE ARRANGED AS FOLLOWS:
 - * EVERY HORIZONTAL JOINT.
 - * BELOW OPENINGS.
 - * ABOVE OPENINGS.
 6. LINTEL BEAM MUST BE PROVIDED ABOVE ALL OPENINGS WITH MIN. 500 MM BEARING
 7. WALL TIES:
NAILED TO CONCRETE COLUMNS/BEAMS
 8. FREE TOP COURSE TO BE ESTABLISHED ON REINFORCED CONCRETE FILLED WITH LINTEL BLOCKS.
 9. GROUT MATERIAL FOR MASONRY SHALL CONFORM TO ASTM C476.
 10. RCC GROUT FILLING AND REINFORCEMENT BARS TO BE ADJUSTED ON SITE TO SUIT LOCATION OF OPENINGS IN THE MASONRY.
 11. EXTERNAL WALL WITH INSULATION: CONTRACTOR TO PROVIDE INSULATION ON EXTERNAL WALLS, WHEREVER INDICATED IN THE FLOOR PLANS.

		Ma'aden Phosphate 3 – Phase 1		
NAME		TITLE	SIGN	DATE
			Mohammad Al Rowaily	
REVIEW GRADE				
Result	Code	Description		
☒		Accepted		
☐	C	Proceed with exceptions to next Submission and Revision		
☐	R	Do Not Proceed - Revise as noted and Resubmit		
Acceptance in any of these categories in no way relieves the Contractor/Supplier of its responsibility for the due and proper performance of the Works in accordance with the Contract/Purchase Order.				
PROJECT MANAGER SIGN-OFF:				
NAME				DATE

REFERENCE DRAWING	
DOCUMENT NUMBER	REFERENCE DOCUMENTS
MD-520-1000-EG-AR-CRT-0001	ARCHITECTURAL DESIGN CRITERIA
MD-101-1000-EG-AR-SPC-00001	ARCHITECTURAL BUILDING MATERIALS SPECIFICATION
-	-
-	-

ISSUED FOR CONSTRUCTION

H												PROPRIETARY & CONFIDENTIAL												"Contractor Insignia to be placed here if applicable"												  												DRAWN D.Agrahari 29-NOV-24												Ma'aden Phosphate 3 Phase I RAK & WAS ARCHITECTURAL STANDARDS WALL DETAILS	
																																				CHECKED S.Suthar 29-NOV-24	
																																				ENGINEER R.Desai 29-NOV-24	
																																				APPROVED B.Mistry	
																																				EMPLOYER MA'ADEN -	
C01 24-APR-25 ISSUED FOR CONSTRUCTION												DCA SPS RUD BDM MA'ADEN																								DRAWING NUMBER												REV	
A01 11-FEB-25 ISSUED FOR REVIEW												NRJ SPS RUD BDM MA'ADEN																								MD-520-1000-EG-AR-STD-0001												C01	
REV DATE REVISION DESCRIPTION												DRN CHK ENG APP EMP	