


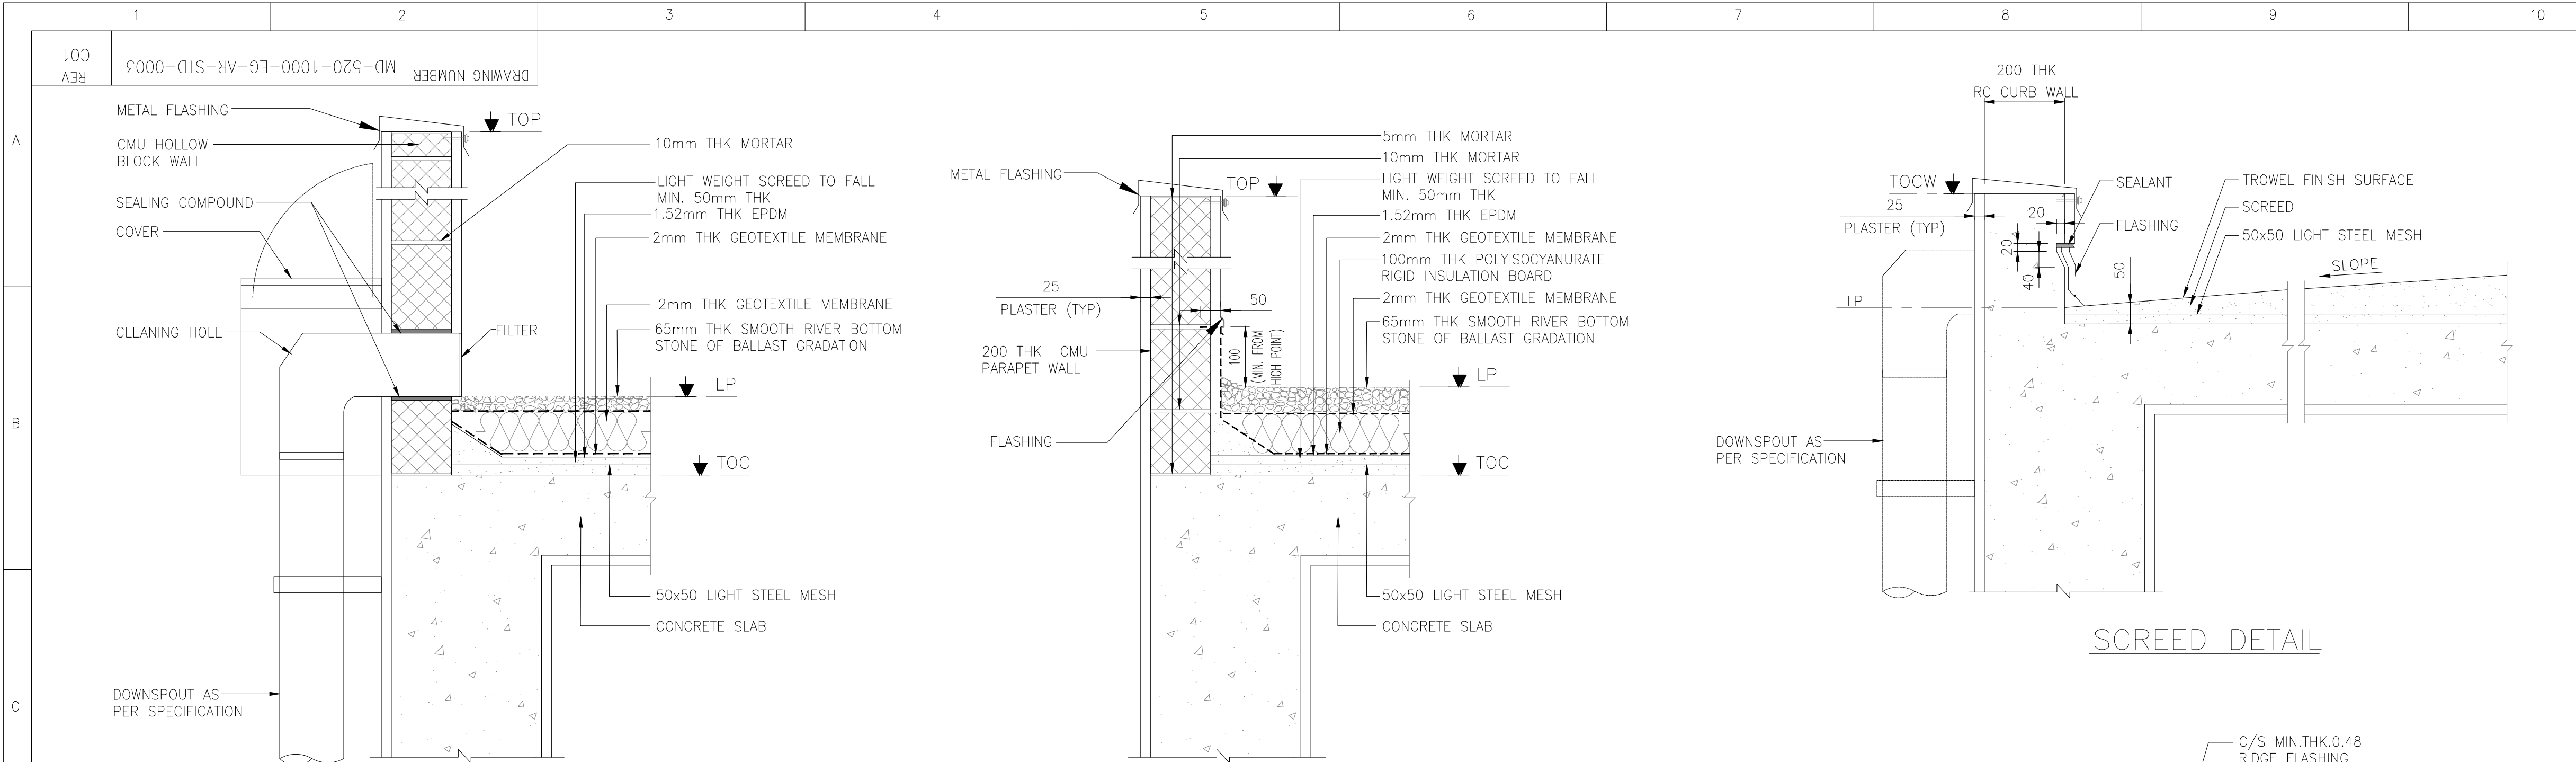


TYPICAL DETAIL FOR
RAIN WATER DOWNSPOUT


TYPICAL WATER PROOFING DETAIL

SCREED DETAIL


RIDGE DETAIL

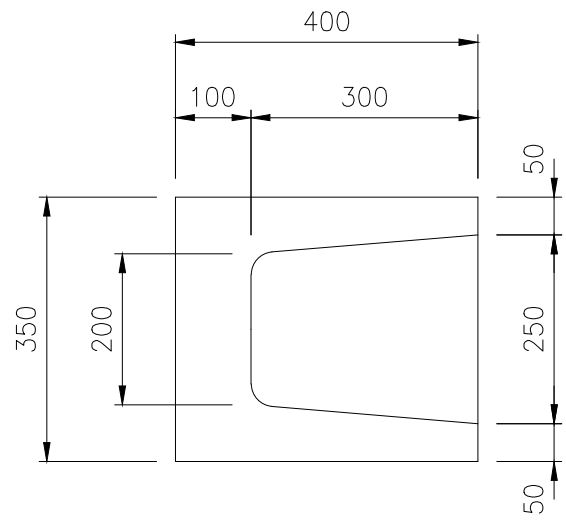

PLAN

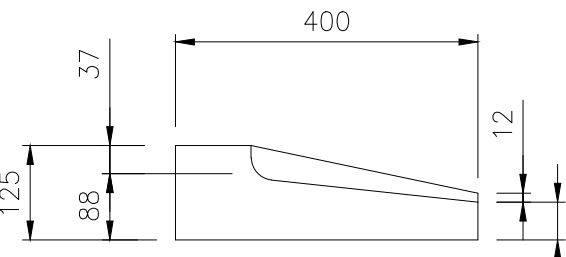


SIDE VIEW

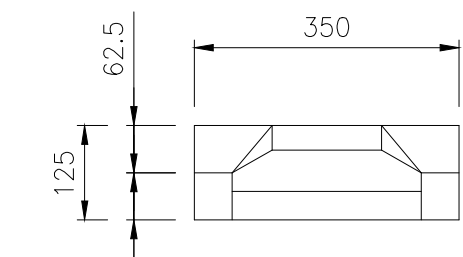


FRONT VIEW

SPLASH BLOCK DETAIL

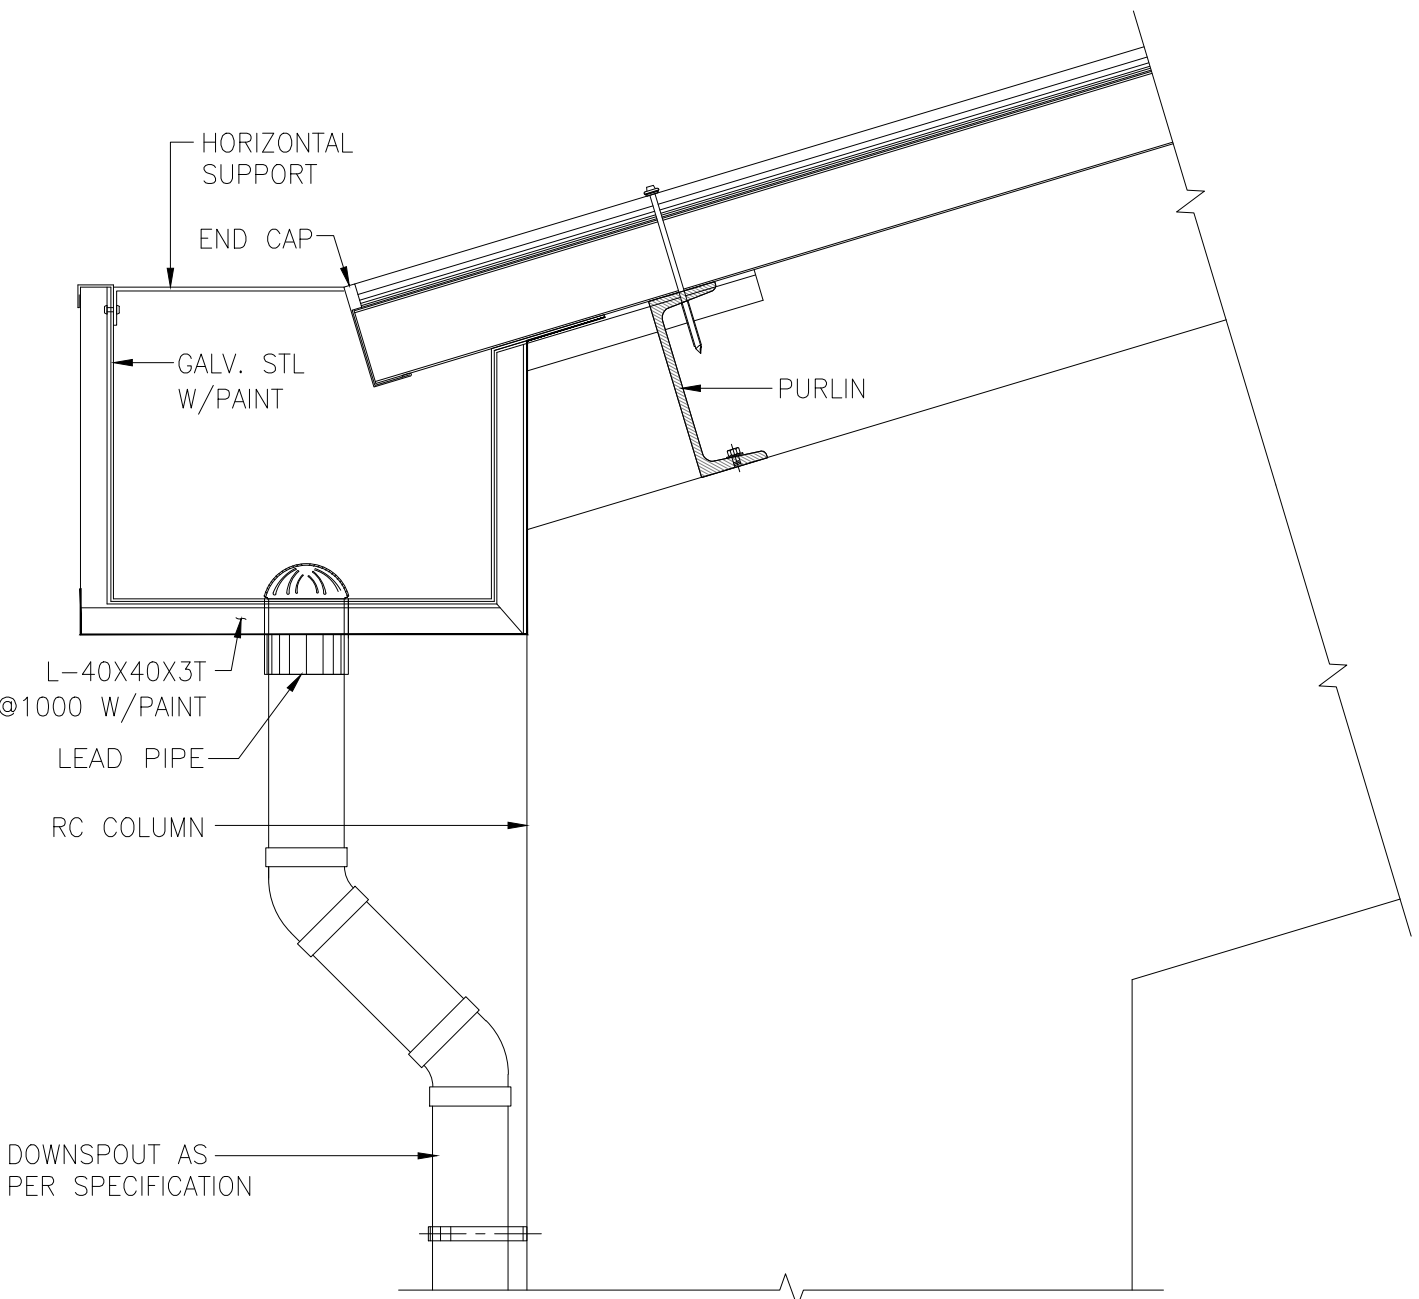

TYPICAL SECTION FOR RAIN GUTTER DETAIL
AND DOWN SPOUT

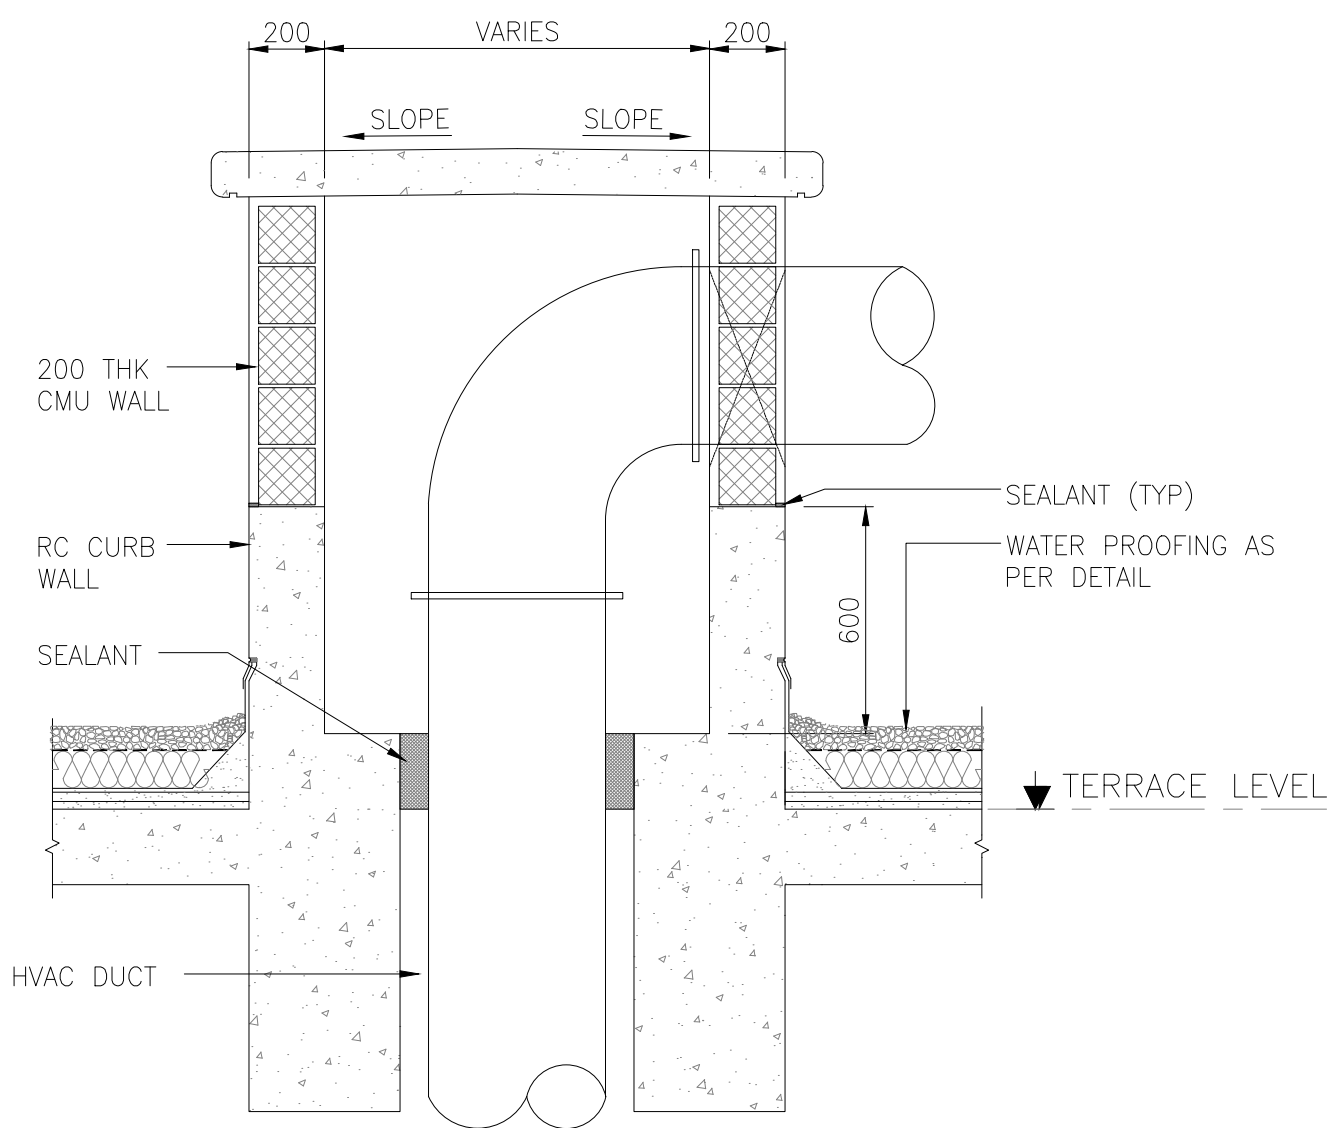

ROOF DUCT OPENING DETAIL

GENERAL NOTES:

1) ALL TYPICAL DETAILS SHALL BE READ IN CONJUNCTION WITH ARCHITECTURAL DRAWINGS.

LEGEND & ABBREVIATION:

		Ma'aden Phosphate 3 – Phase 1	
NAME	TITLE	SIGN	DATE
REVIEW GRADE			
Result	Code	Description	
☐	A	Accepted	
☐	C	Proceed with exceptions to next Submission and Revision	
☐	R	Do Not Proceed - Revise as noted and Resubmit	
Acceptance in any of these categories in no way relieves the Contractor/Supplier of its responsibility for the due and proper performance of the Works in accordance with the Contract/Purchase Order.			
PROJECT MANAGER SIGN-OFF:			
NAME		DATE	

REFERENCE DRAWING	
DOCUMENT NUMBER	REFERENCE DOCUMENTS
MD-520-1000-EG-AR-CRT-0001	ARCHITECTURAL DESIGN CRITERIA
MD-101-1000-EG-AR-SPC-00001	ARCHITECTURAL BUILDING MATERIALS SPECIFICATION
-	-
-	-

ISSUED FOR CONSTRUCTION

REV	DATE	REVISION DESCRIPTION	DRN	CHK	ENG	APP	EMP
C01	03-APR-25	ISSUED FOR CONSTRUCTION	DCA	SPS	RUD	BDM	MA'ADEN
A01	11-FEB-25	ISSUED FOR REVIEW	NRJ	SPS	RUD	BDM	MA'ADEN

PROPRIETARY & CONFIDENTIAL

This document and the information contained herein is Ma'aden proprietary know-how. This document or any part thereof should not be reproduced, stored in a retrieval system or transmitted by any means, electronic or otherwise, or divulged without prior written permission of Ma'aden.

"Contractor Insignia to be placed here if applicable"



DRAWN	D.Agrahari	29-NOV-24
CHECKED	S.Suthar	29-NOV-24
ENGINEER	R.Desai	29-NOV-24
APPROVED	B.Mistry	
EMPLOYER	MA'ADEN	-
SCALE	NTS	A1

Ma'aden Phosphate 3 Phase I RAK & WAS ARCHITECTURAL STANDARDS ROOF & WATERPROOFING DETAILS	
DRAWING NUMBER MD-520-1000-EG-AR-STD-0003	REV C01