
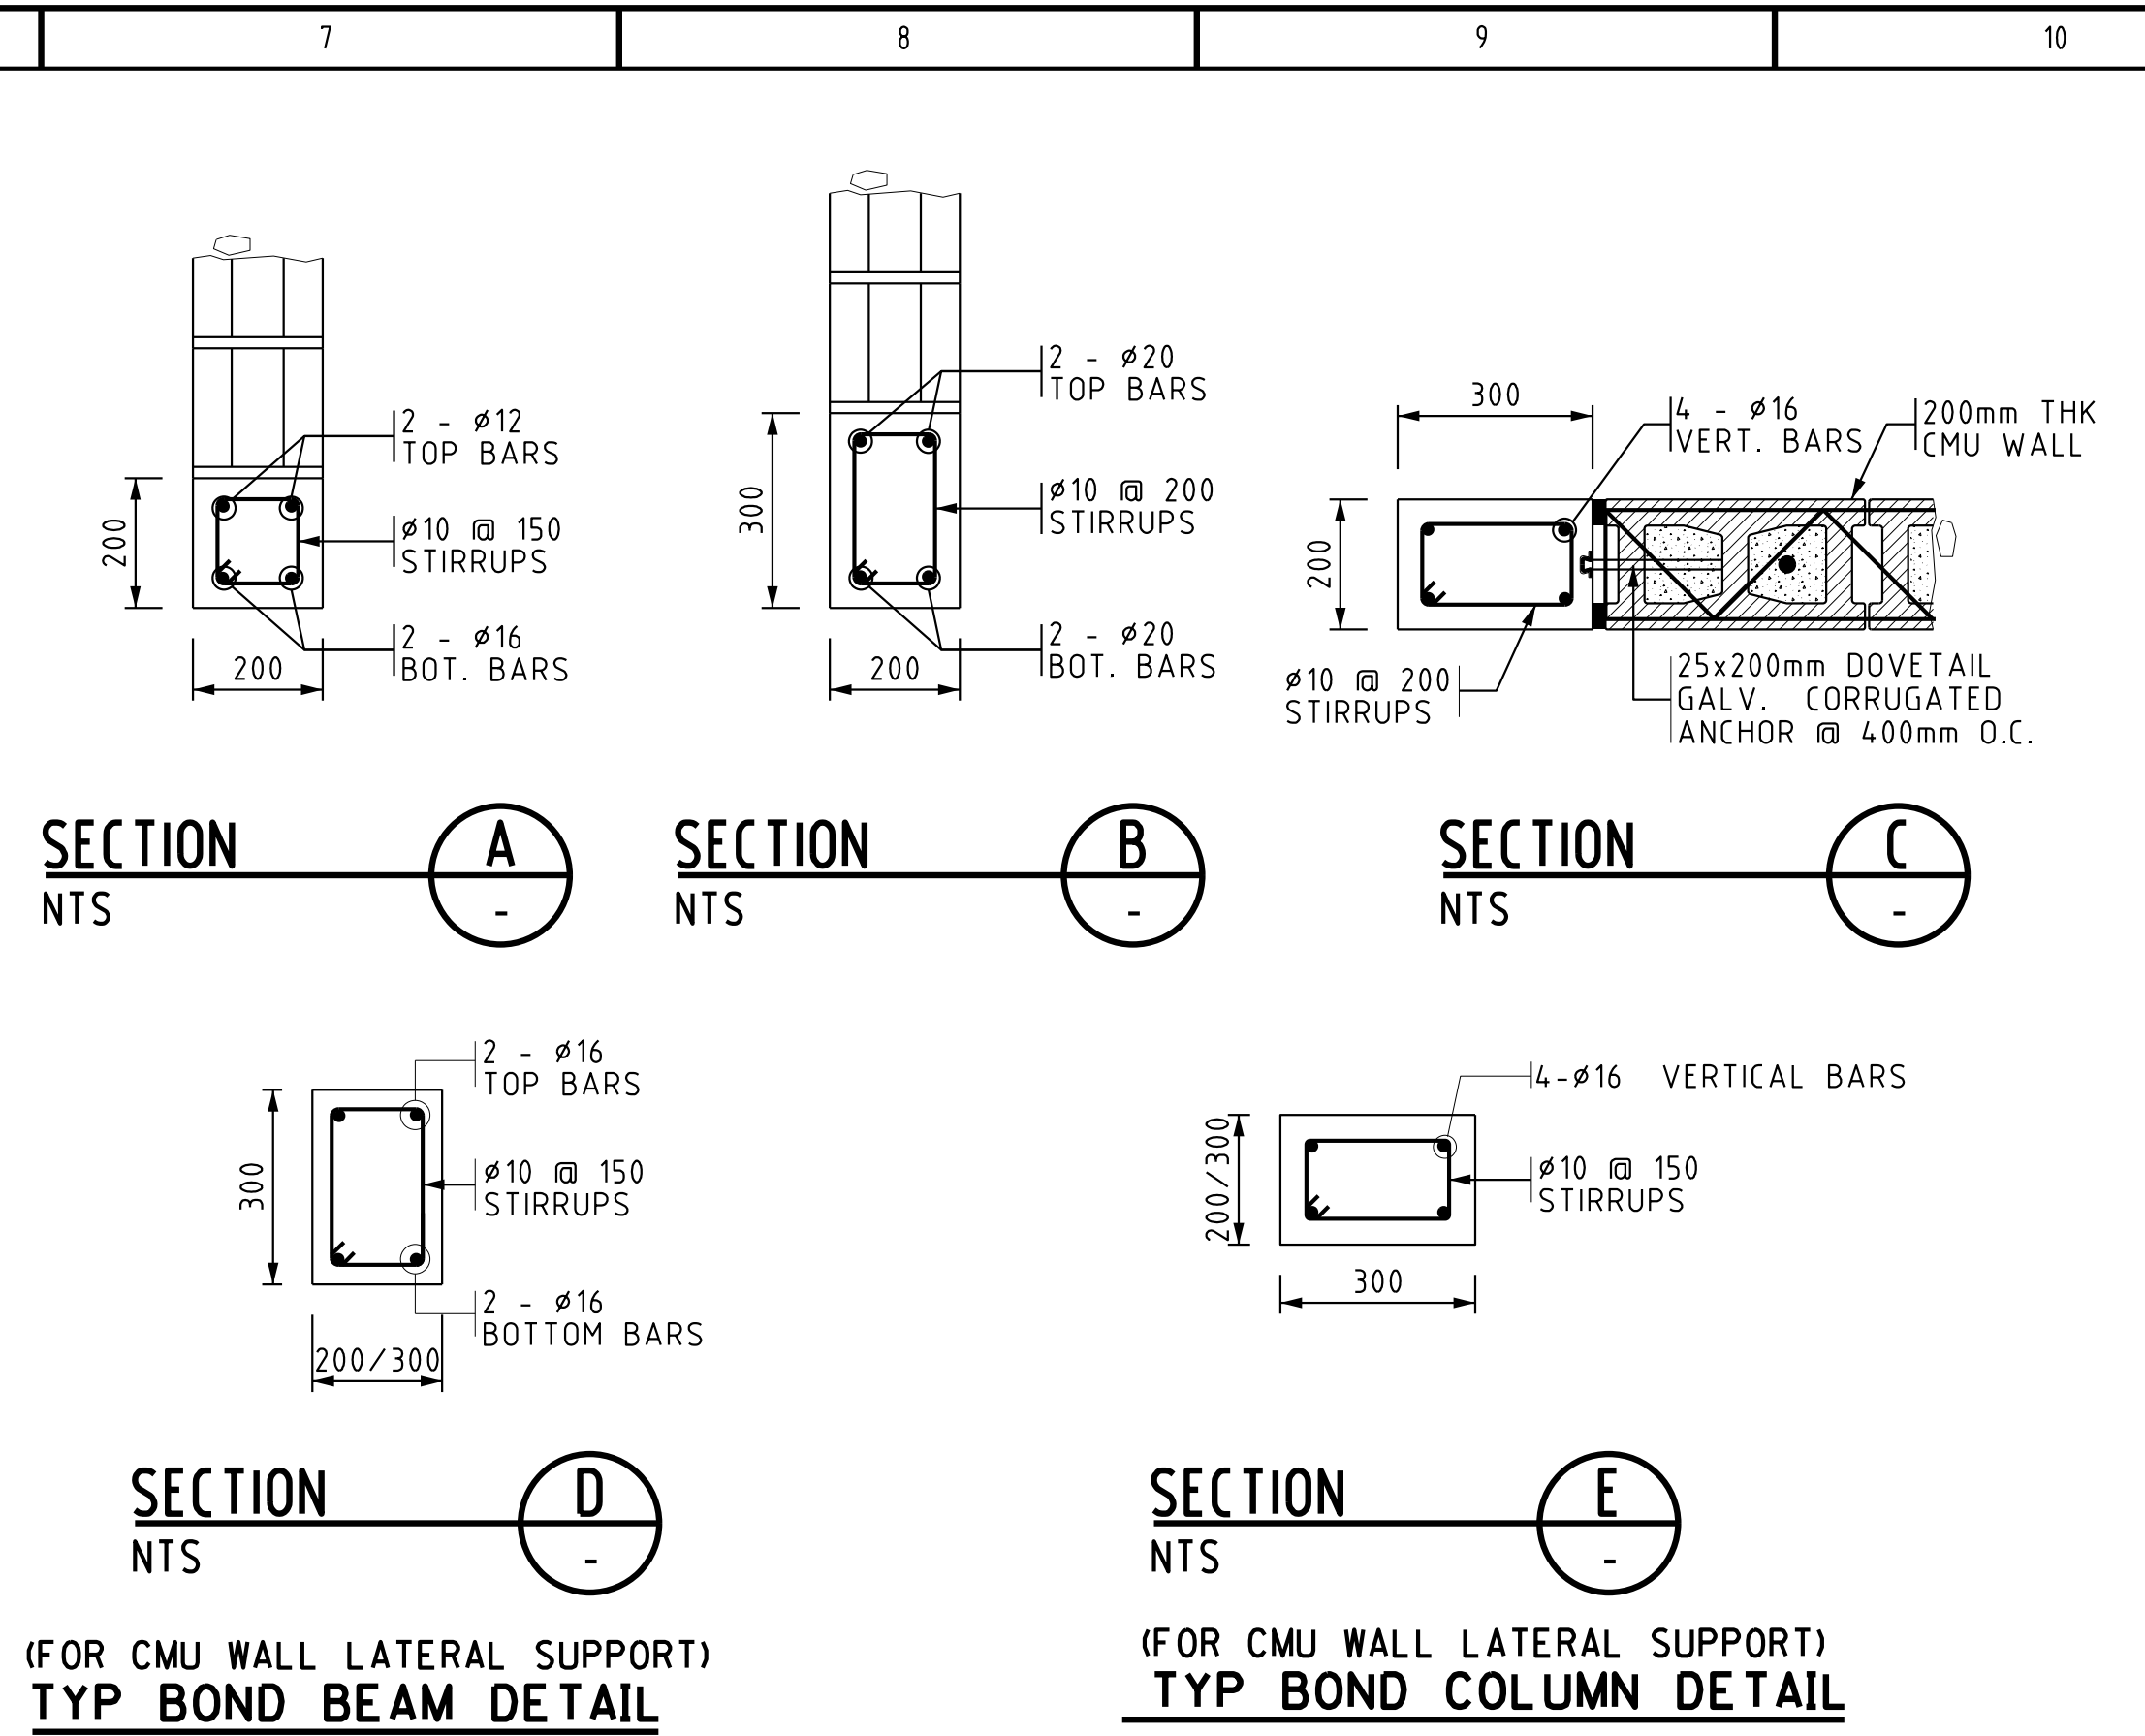


06-Oct-24 10:37:49 AM \\saalkw\pds01\Projects\Projects\WPE\CC_Projects\303011\Infra\313011-002823\11_Buildings_Scope\1114_Buildings_Scope\1114_09_Structural\2.0_RAK\1.0_Working_Folder\GENERAL_DRAWING\MD-520-1000-EG-ST-STD-0021-L01.dgn

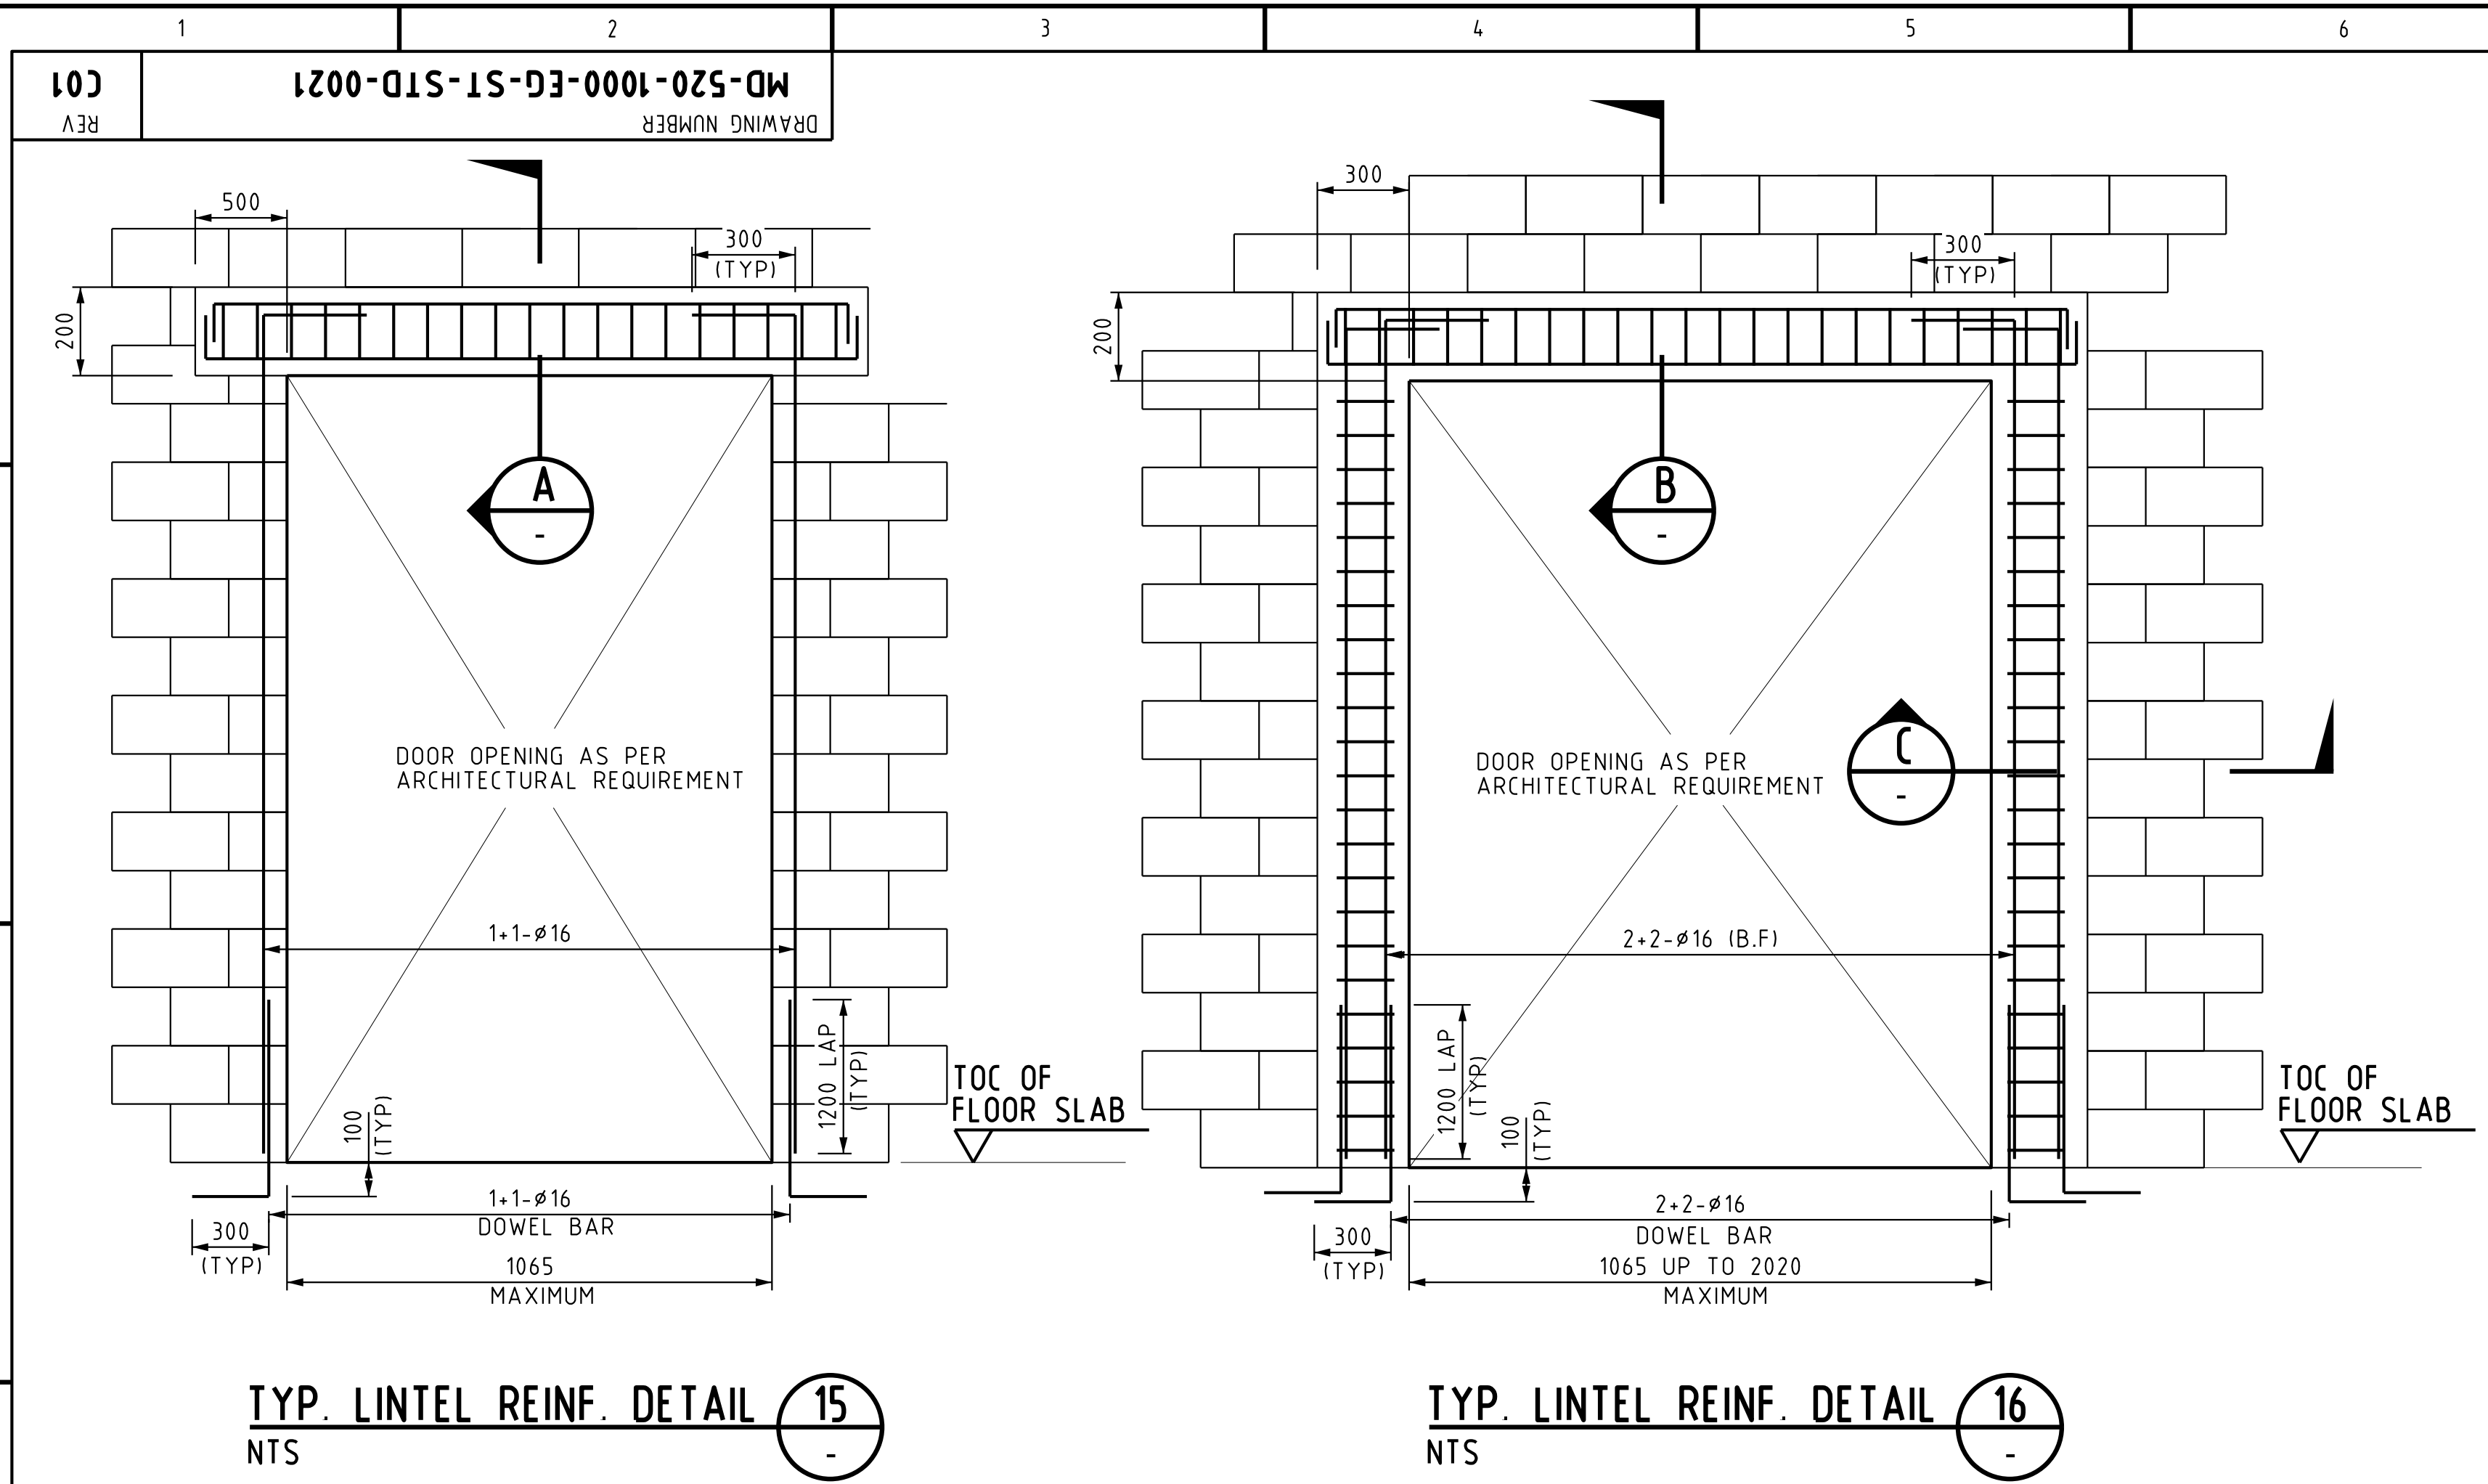

- GENERAL NOTES:**
- ALL DIMENSIONS ARE IN MILLIMETERS. ALL LEVELS ARE IN METERS UNLESS OTHERWISE NOTED.
 - FOR OTHER NOTES REFER STRUCTURAL GENERAL NOTES DRAWING NO. MD-520-1000-EG-CV-STD-0001.
 - AS PER ACI 530 TABLE 5.5.1, MAXIMUM SPACING OF PILLASTER AND BOND BEAM FOR EXTERNAL CMU WALLS SHALL BE 18 TIMES WALL THICKNESS (18 x T) AND FOR INTERNAL CMU WALLS ITS SHALL BE 36 TIMES WALL THICKNESS (36 x T). WHERE T IS THICKNESS OF CMU WALL.


- LEGEND AND ABBREVIATIONS:**
- TOC - TOP OF CONCRETE
TYP - TYPICAL
BOT. - BOTTOM
VERT. - VERTICAL

HOLDS:

REFERENCE DRAWING	
DOCUMENT NUMBER	REFERENCE DOCUMENTS
MD-520-1000-EG-CV-STD-0001	STRUCTURAL CONCRETE GENERAL NOTES
MD-520-1000-EG-ST-STD-0016 TO 0020	NPB TYPICAL STRUCTURAL DETAILS
MD-520-1000-EG-ST-STD-0022 & 0023	NPB TYPICAL STRUCTURAL DETAILS

Ma'aden Phosphate 3 - Phase 1			
NAME	TITLE	SIGN	DATE
REVIEW GRADE			
Result	Code	Description	
☐	A	Accepted	
☐	C	Proceed with exceptions to next Submission and Revision	
☐	R	Do Not Proceed - Revise as noted and Resubmit	
Acceptance in any of these categories in no way relieves the Contractor/Supplier of its responsibility for the due and proper performance of the Works in accordance with the Contract/Purchase Order.			
PROJECT MANAGER SIGN-OFF:			
NAME		DATE	

ISSUED FOR CONSTRUCTION

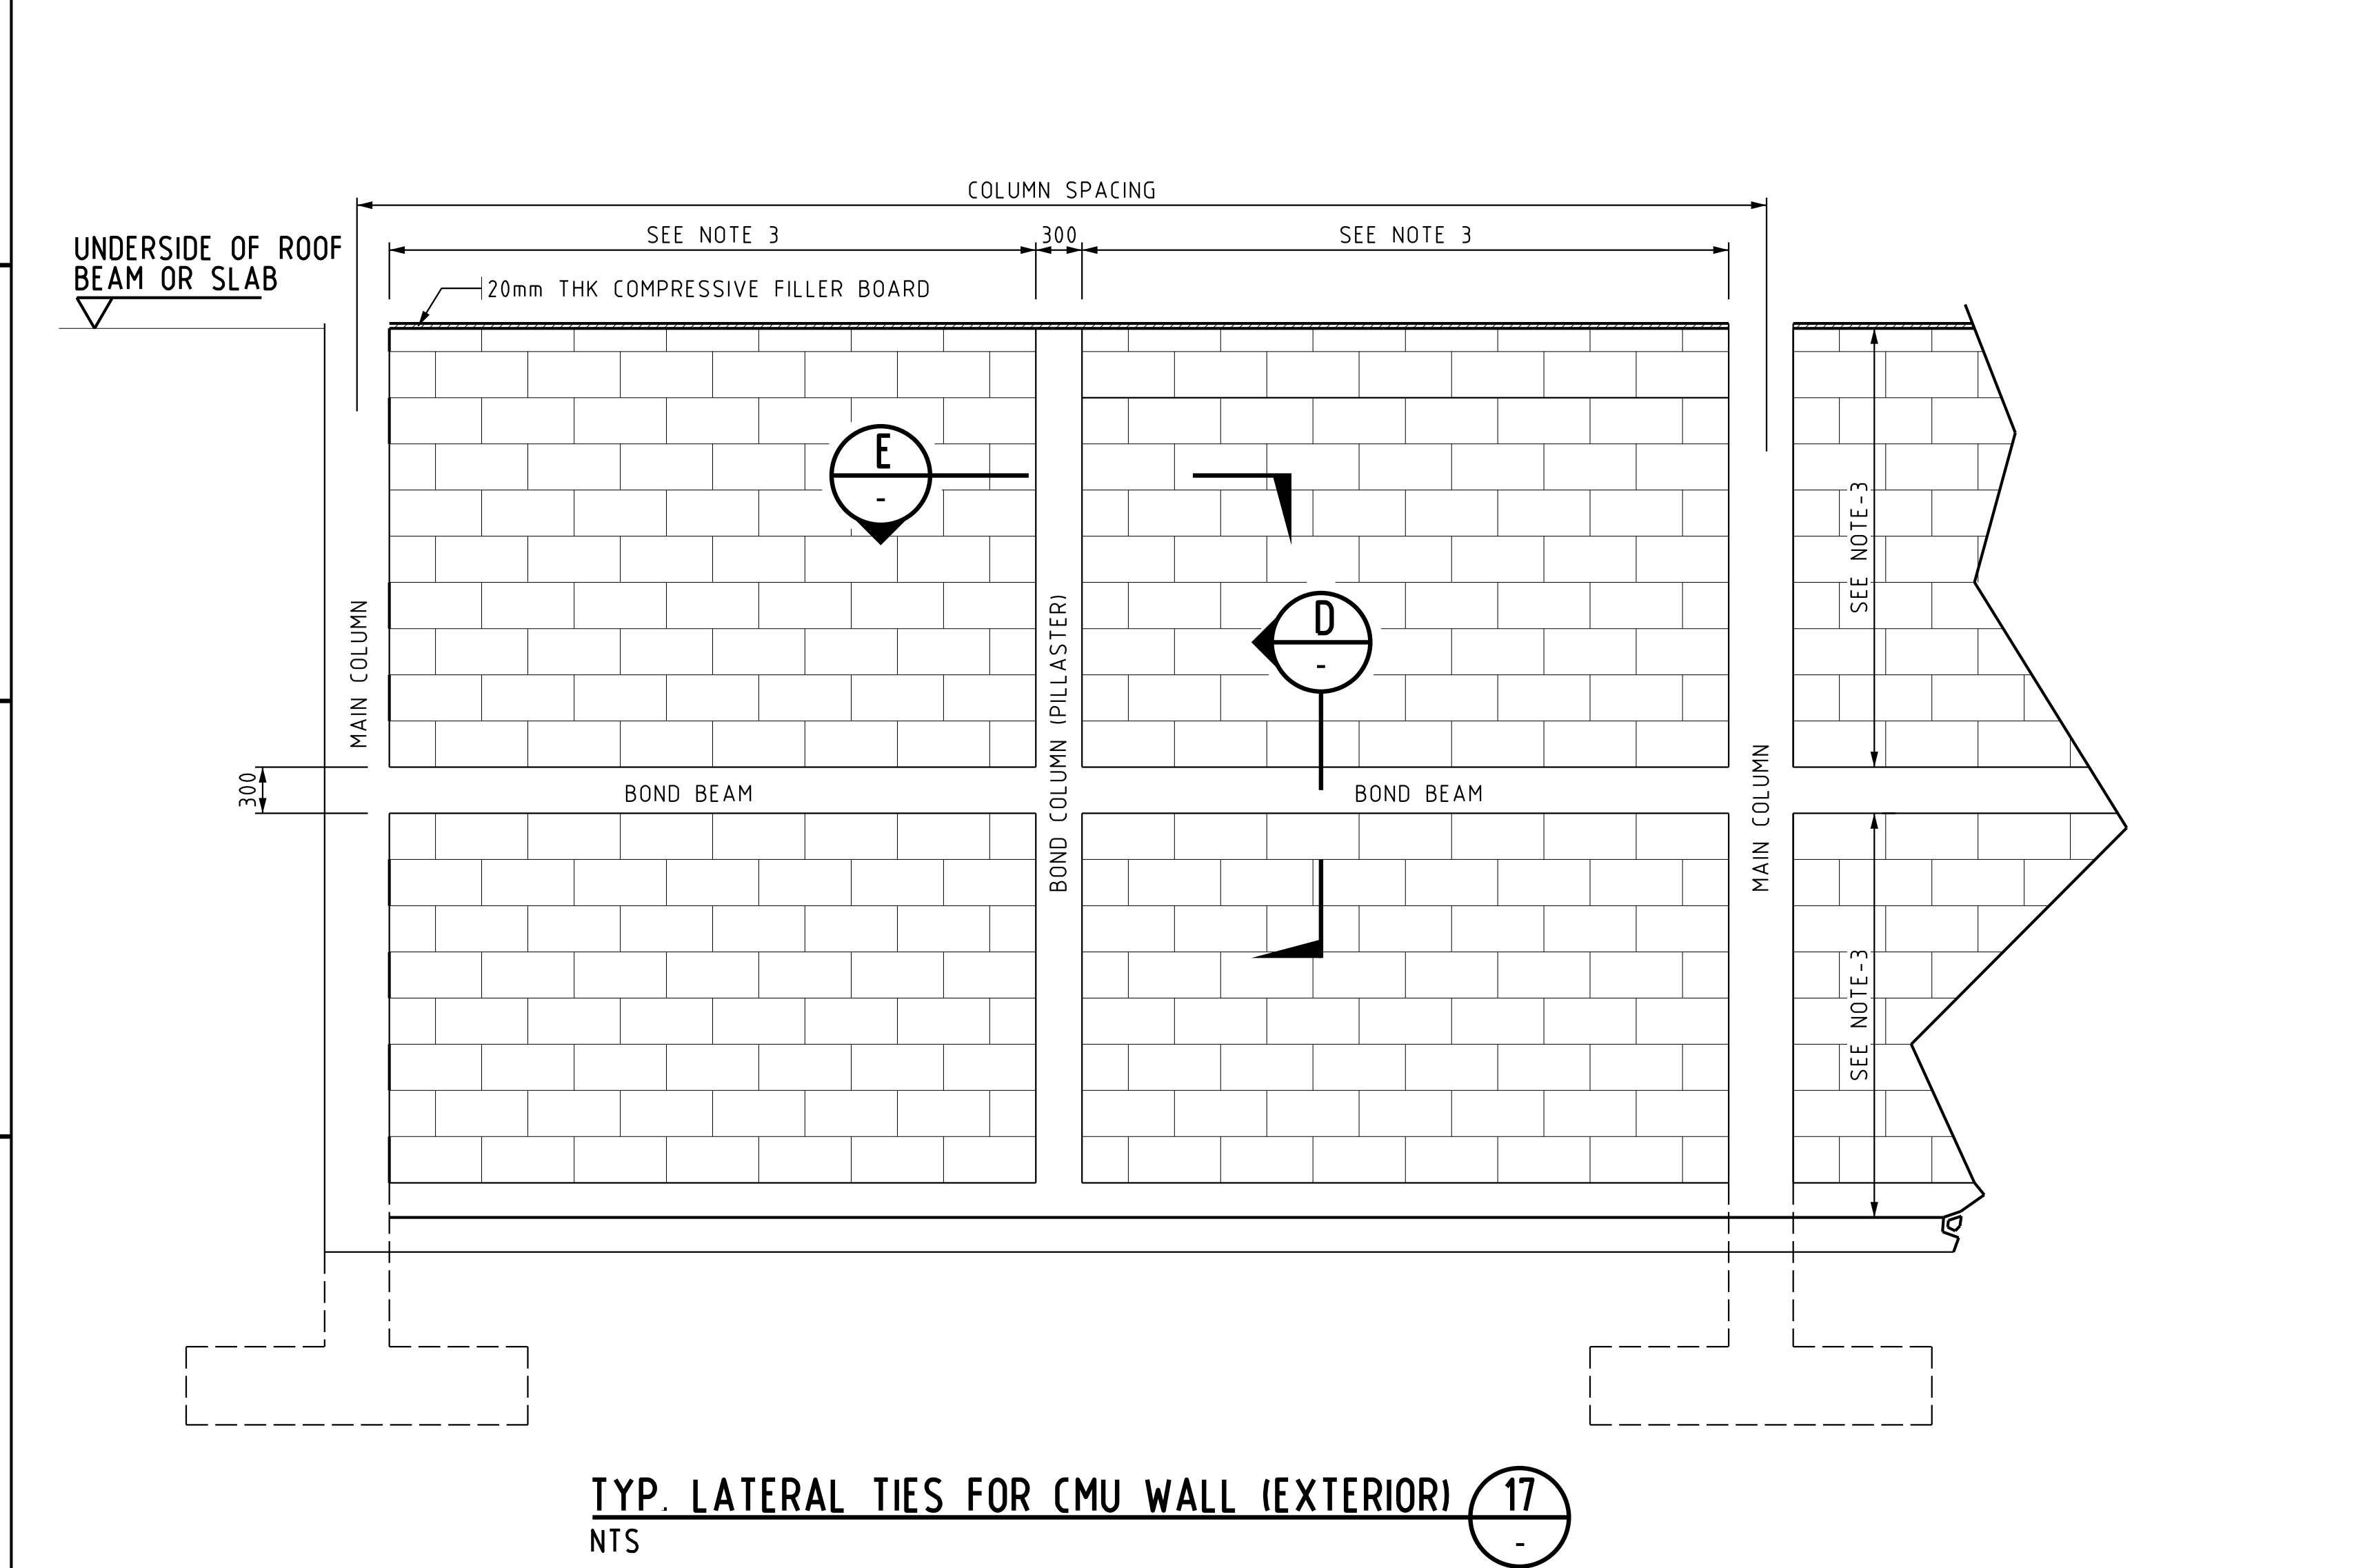

REV	DATE	REVISION DESCRIPTION	DRN	CHK	ENG	APP	EMP
C01	17/09/24	ISSUED FOR CONSTRUCTION	JS	YK	RC	UC	MD
A01	03/01/24	ISSUED FOR REVIEW	PP	YK	RC	UC	MD

PROPRIETARY & CONFIDENTIAL

This document and the information contained herein is Ma'aden proprietary know-how. This document or any part thereof should not be reproduced, stored in a retrieval system or transmitted by any means, electronic or otherwise, or divulged without prior written permission of Ma'aden.



DRAWN	P. PEDNEKAR	03/01/24
CHECKED	Y. KHAN	03/01/24
ENGINEER	R. CHERUVU	03/01/24
APPROVED	U. CHAUDHARI	03/01/24
EMPLOYER	MA'ADEN	03/01/24
SCALE	NTS	A1

**MA'ADEN PHOSPHATE 3 PHASE-1
RAS AL KHAIR AND WAAD AL SHAMAL
NPB TYPICAL CMU WALL DETAILS**

DRAWING NUMBER	REV
MD-520-1000-EG-ST-STD-0021	C01