

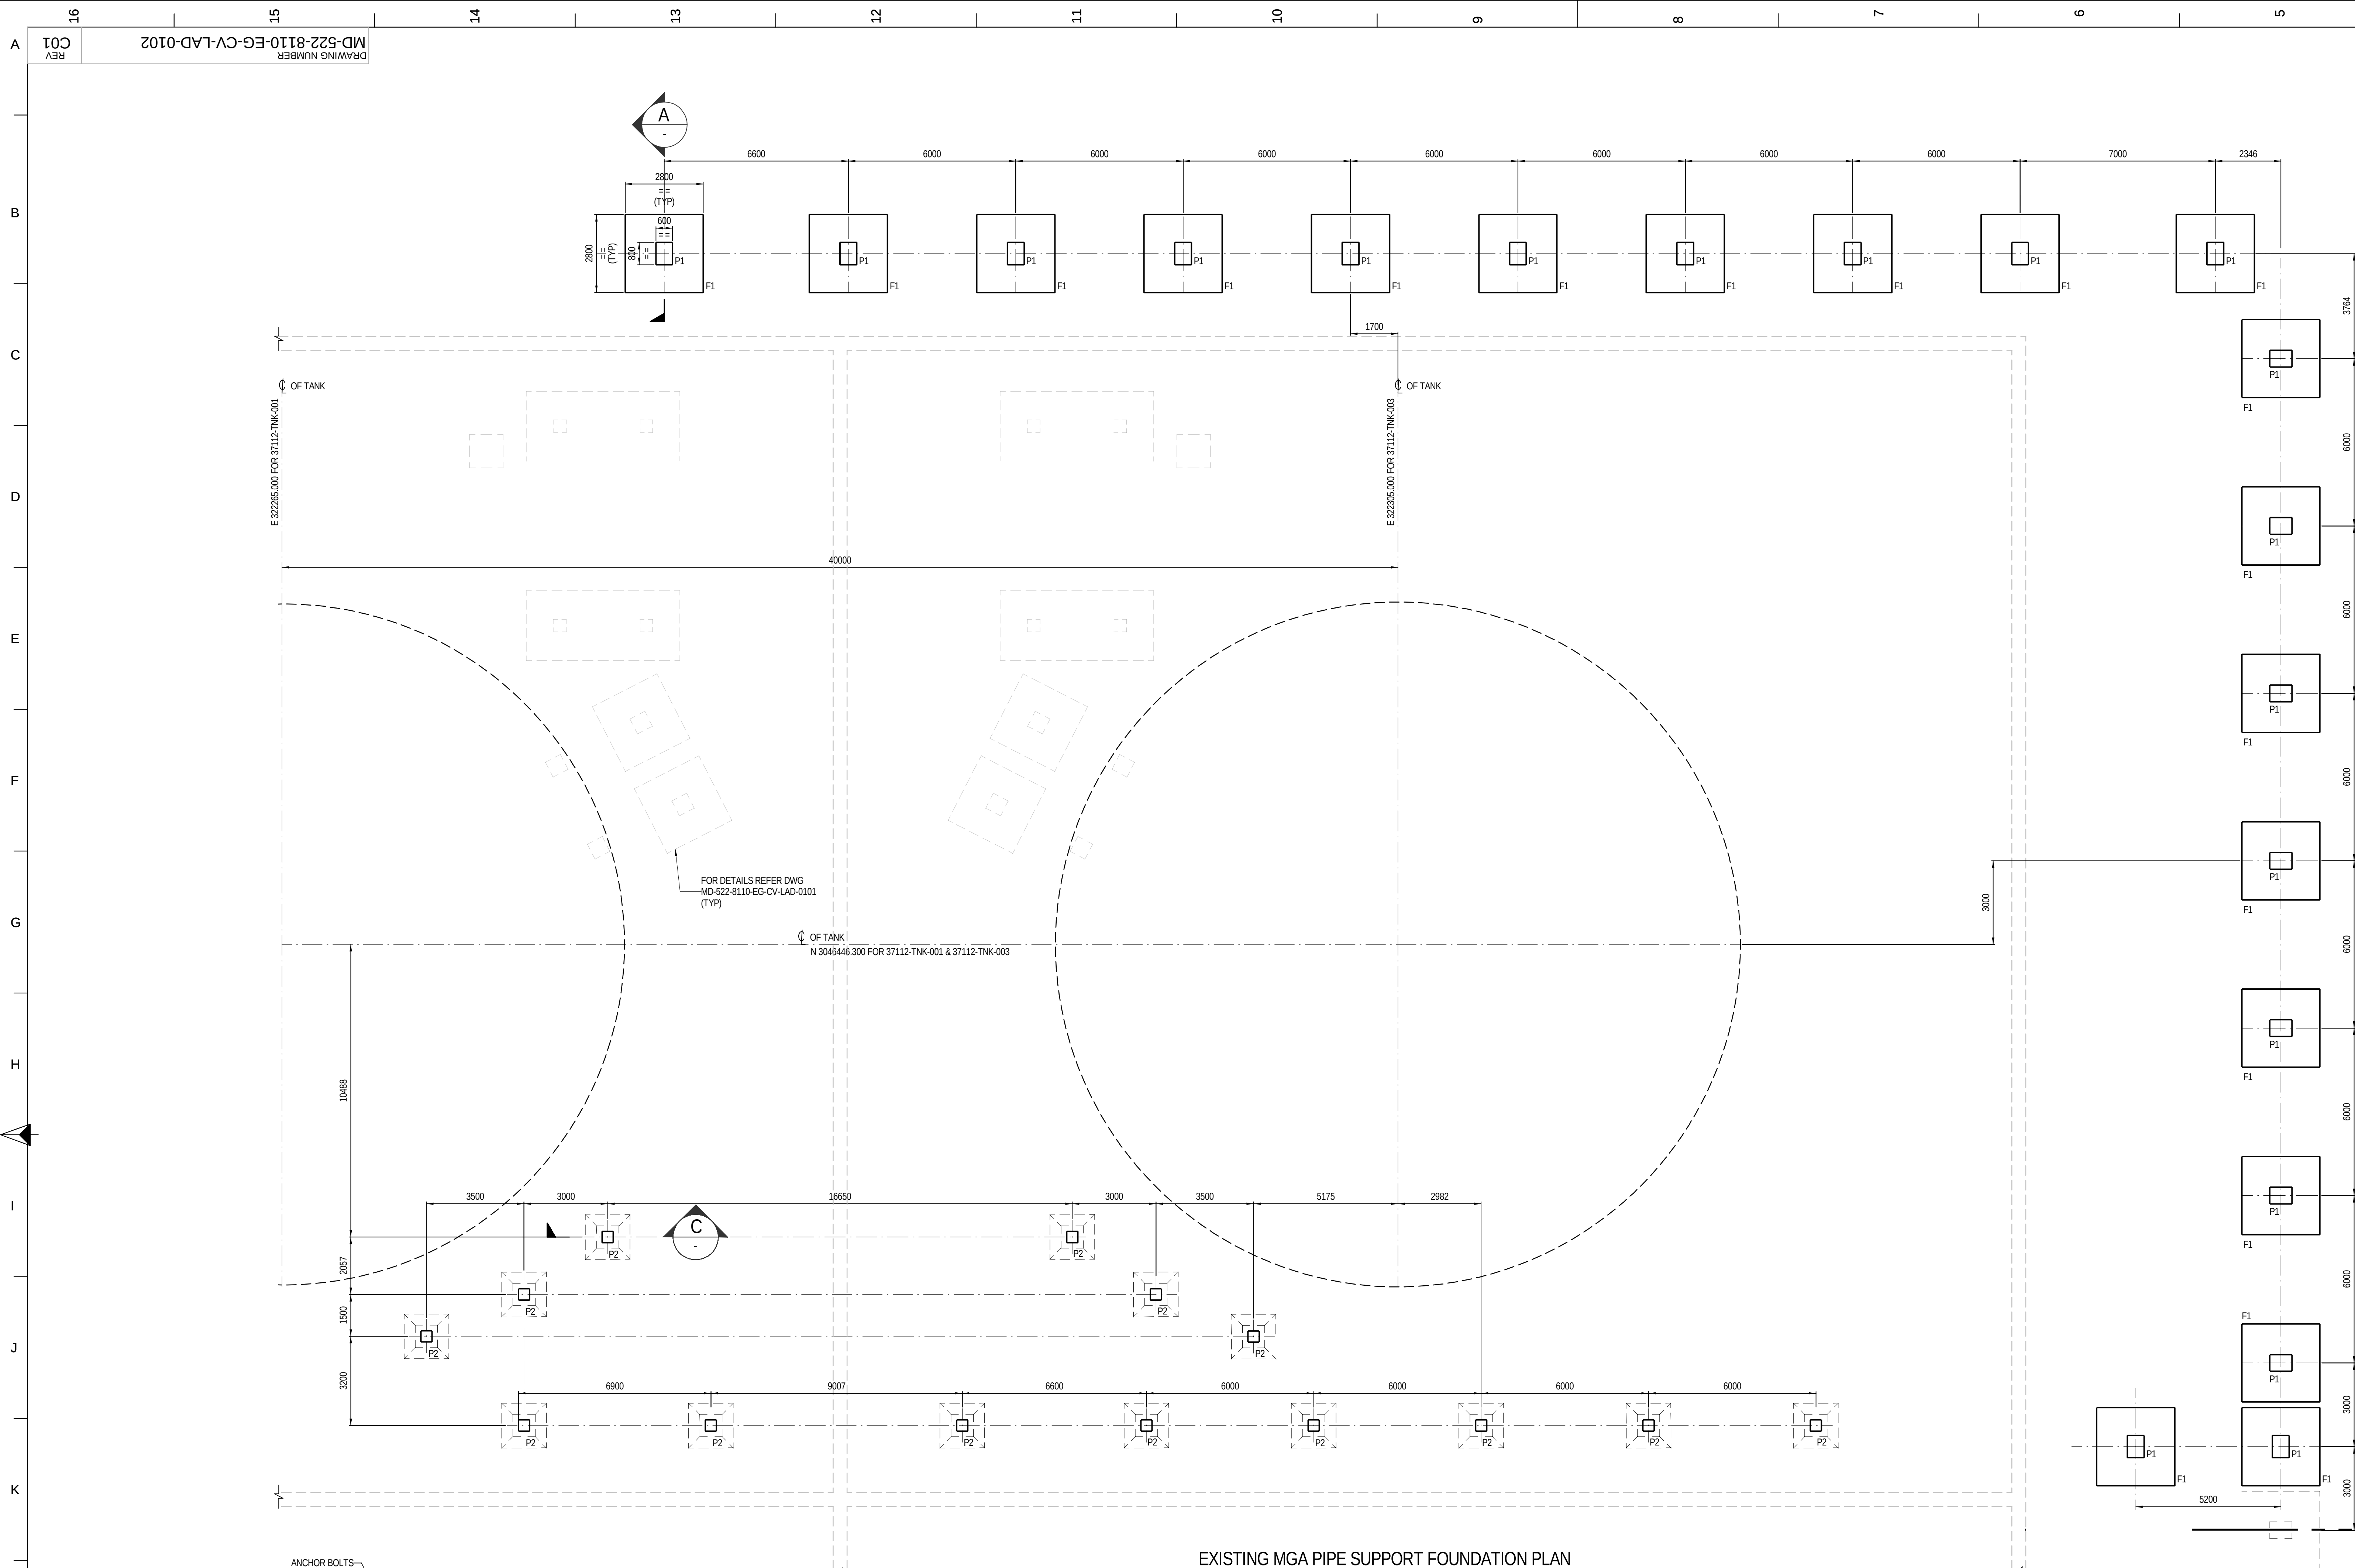
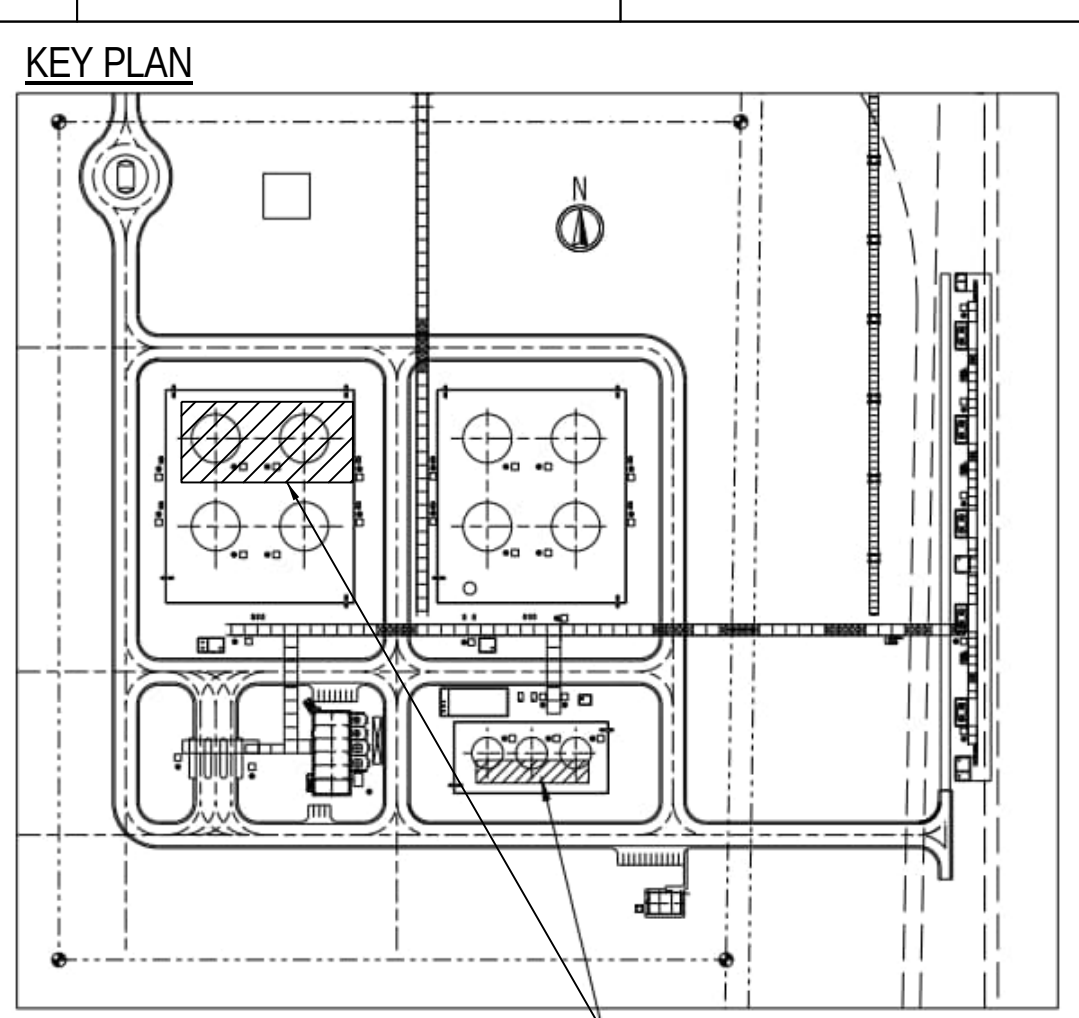
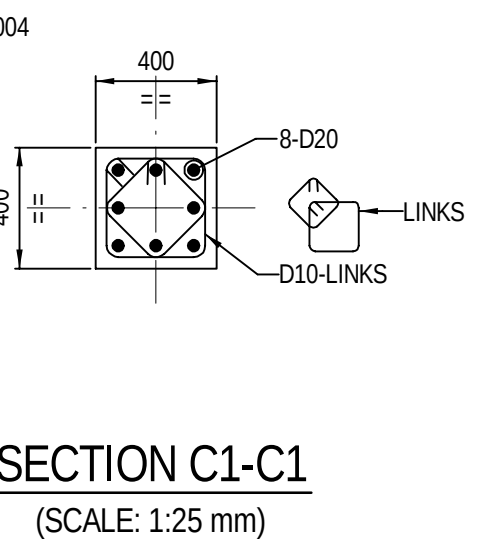
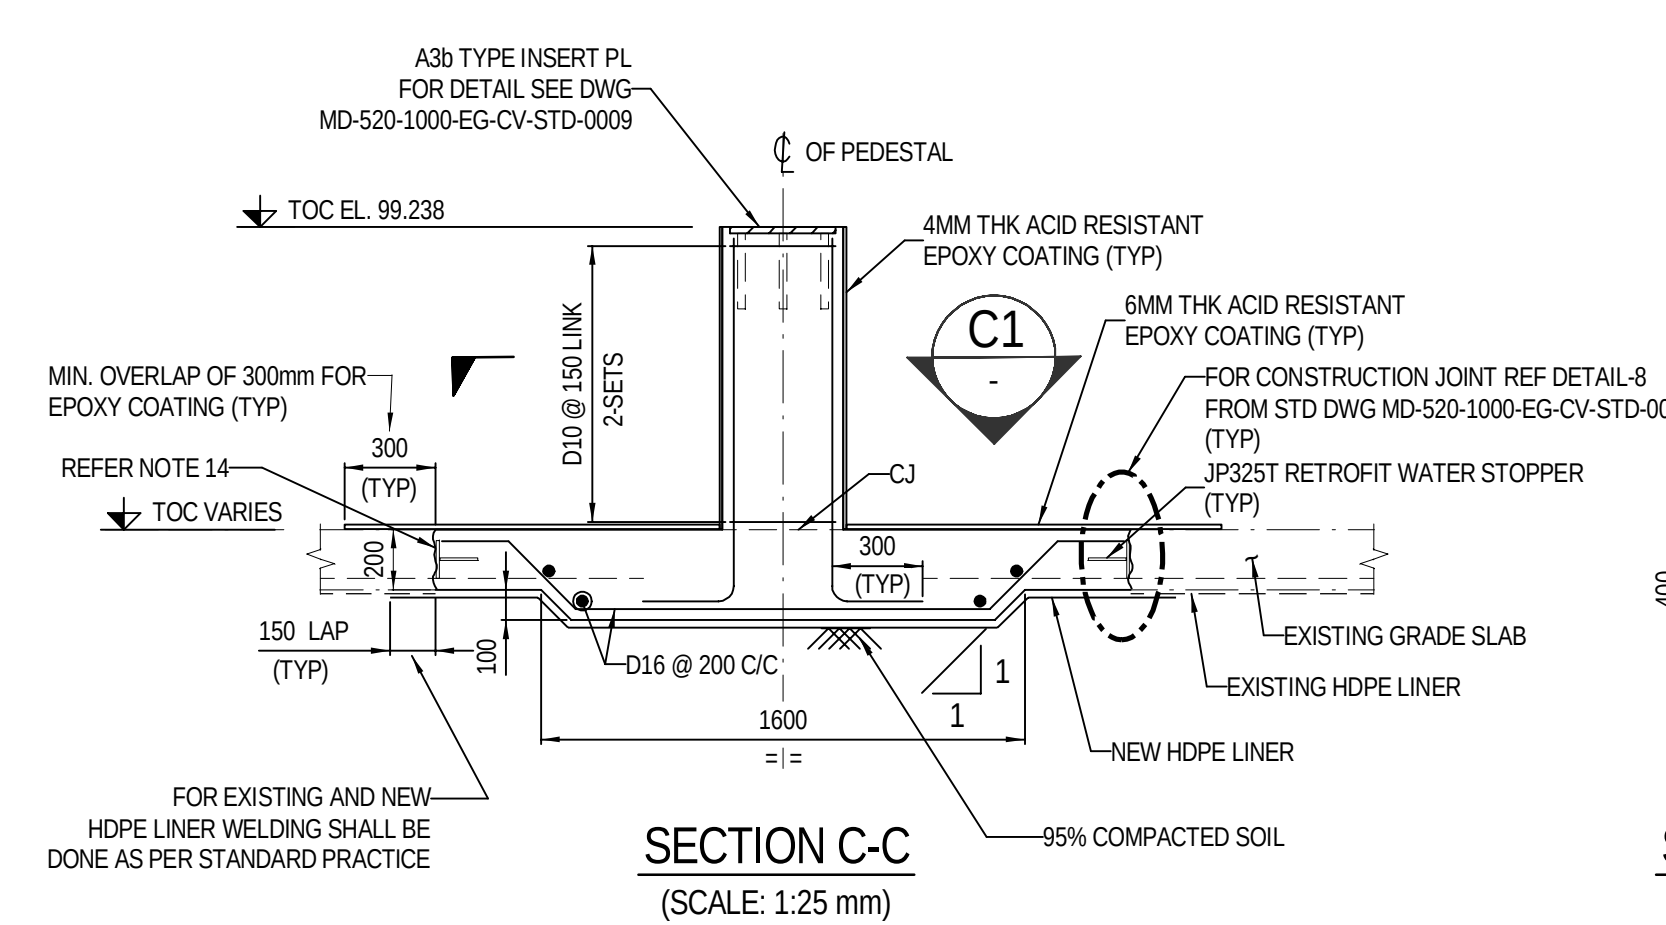


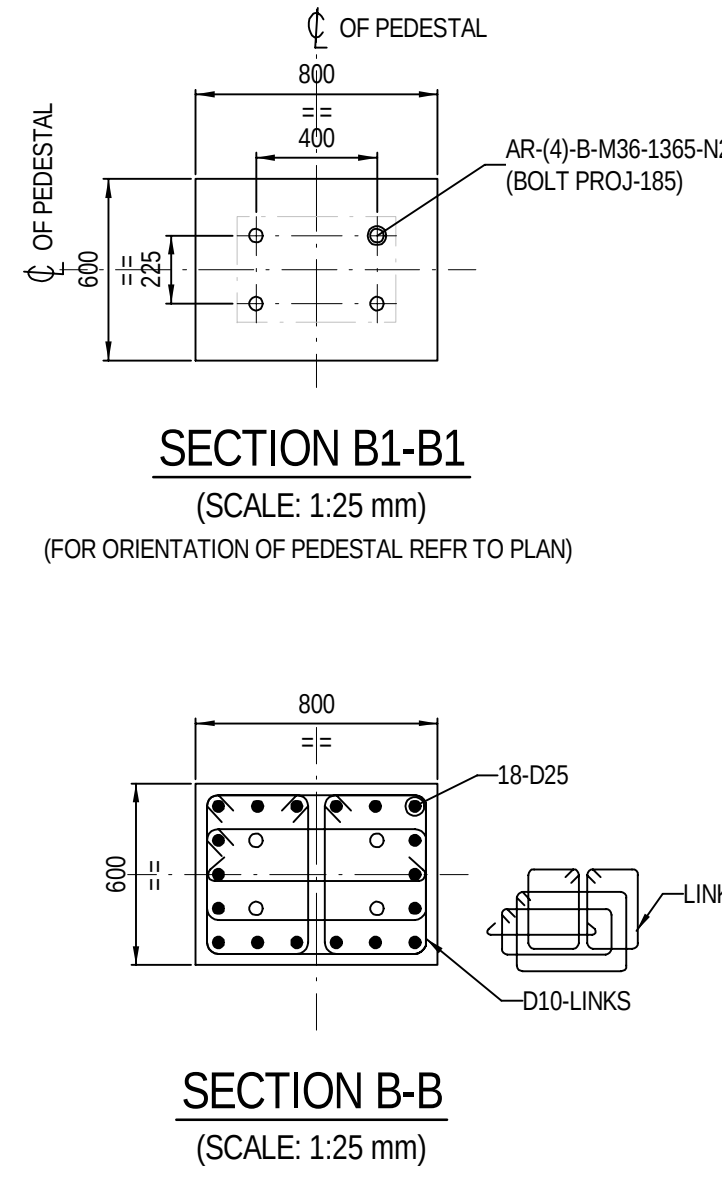

MATCHLINE CONT ON DWG
MD-522-8110-EG-CV-LAD-0103

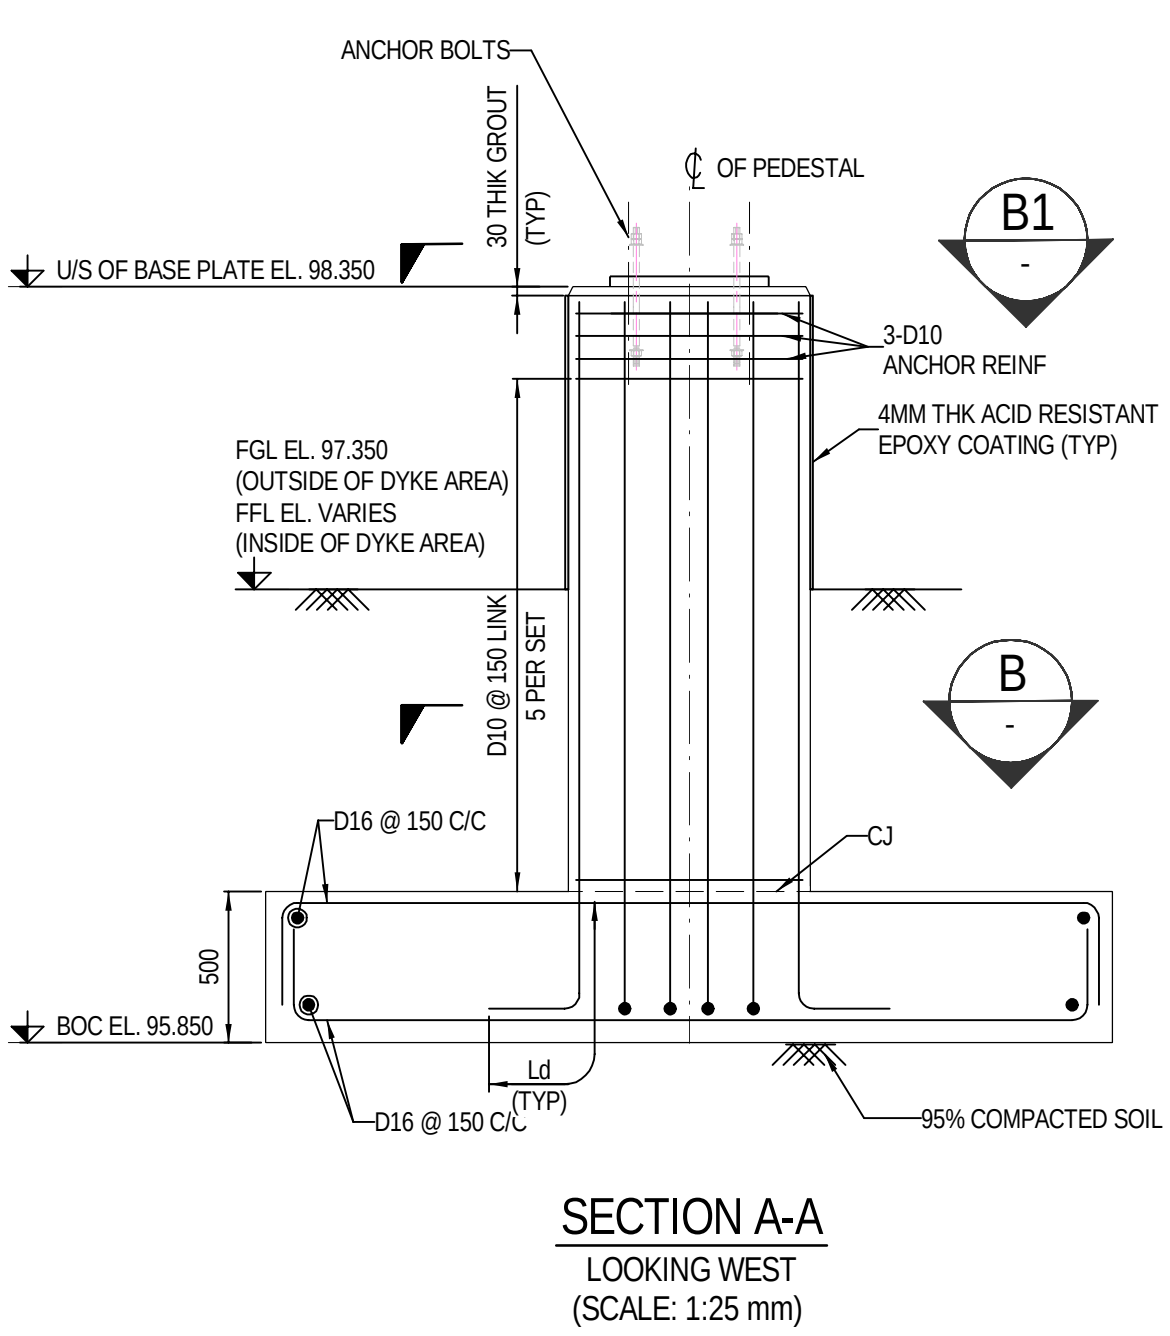

- NOTES:-**
1. ALL DIMENSIONS ARE IN MILLIMETERS, LEVELS (ELEVATIONS) AND COORDINATES ARE IN METERS UNLESS NOTED OTHERWISE.
 2. FOR REFERENCES SEE DWG MD-522-8110-EG-CV-LAD-0101.
 3. ALL COORDINATES ARE BASED ON UTM 38R COORDINATE SYSTEM.
 4. FOR GENERAL CONCRETE NOTES REFER DWG NO. MD-520-1000-EG-CV-STD-0001.
 5. PLANT ELEVATION EL.100.000+7.00m M.S.L. (COMPANY REFERENCE TO MEAN SEA LEVEL).
 6. BLINDING CONCRETE SHALL HAVE MINIMUM SPECIFIED STRENGTH OF 15 N/mm² AS PER GENERAL SPECIFICATION FOR CONCRETE CONSTRUCTION.
 7. THE TYPE OF CEMENT MUST FOLLOW THE DEFINITION IN THE GEOTECHNICAL REPORT.
 8. ALL REBARS SHALL BE EPOXY COATED.
 9. CONCRETE MIX SHALL HAVE MINIMUM CYLINDRICAL COMPRESSIVE STRENGTH OF 35 MPa FOR CAST IN SITU CONCRETE.
 10. REINFORCEMENT GRADE SHALL BE 40N/mm² CONFORMING TO ASTM A615M.
 11. FOR ANY CLASHES WITH UG SERVICES, REVERT TO DESIGN OFFICE.
 12. THIS DRAWING IS RELATED TO CONSTRUCTION WORK AREA NUMBER CWA-7113.
 13. ROUGHEN THE SURFACE OF THE EXISTING CONCRETE AND BLOW THE SURFACE CLEAN. THE SURFACE SHALL BE DRY AND FREE OF GREASE.
 14. APPLY EPOXY BASED BONDING AGENT NITOBOND EP OR EQUIVALENT.
 15. POUR NEW CONCRETE AS PER CONCRETE WORK SPECIFICATION.

LEGEND:
NL

		Ma'aden Phosphate 3 – Phase 1		
NAME		TITLE	SIGN	DATE
REVIEW GRADE				
Result	Code	Description		
☐	A	Accepted		
☐	C	Proceed with exceptions to next Submission and Revision		
☐	R	Do Not Proceed - Revise as noted and Resubmit		
Acceptance in any of these categories in no way relieves the Contractor/Supplier of its responsibility for the due and proper performance of the Works in accordance with the Contract/Purchase Order.				
PROJECT MANAGER SIGN-OFF:				
NAME			DATE	

ISSUED FOR CONSTRUCTION

ALL DIMENSIONS AND ELEVATIONS SHALL BE VERIFIED BEFORE STARTING THE CONSTRUCTION, ANY DISCREPANCIES SHALL BE NOTIFIED TO DESIGN TEAM.

DOCUMENT NUMBER	REFERENCE DOCUMENTS	REV	DATE	REVISION DESCRIPTION	DRN	CHK	ENG	APP	EMP
C01	18/08/25			ISSUED FOR CONSTRUCTION					
A01	29/07/25			ISSUED FOR REVIEW (RFR)					

PROPRIETARY & CONFIDENTIAL
This document and the information contained herein is Ma'aden proprietary information. This document or any part thereof should not be reproduced, stored in a retrieval system or transmitted in any form, electronic or otherwise, or divulged without prior written permission of Ma'aden.

"Contractor Insignia to be placed here if applicable"



DRAWN	P.PARDULE	18/07/25
CHECKED	A.KAMTEKAR	18/07/25
ENGINEER	V.SHINDE	18/07/25
APPROVED	V.DHAPATKAR	18/07/25
EMPLOYER	MA'ADEN	
SCALE	--	

REFERENCE DRAWINGS		
MD-522-8110-EG-CV-LAD-0103	EXISTING MGA FOUNDATION LAYOUT PIPE SUPPORT SH-2	CIVIL
MD-522-8110-EG-CV-LAD-0101	EXISTING MGA FOUNDATION LAYOUT	CIVIL
CWP-7113-CV-CF-001	DRG. NO.	TITLE
EWP-7113-CV-CF-001		
MA'ADEN PHOSPHATE 3 PHASE 1 RAK-RAS AL KHAIR-AREA 'A' EXISTING MGA FOUNDATION LAYOUT SH-1 PIPE SUPPORT		
DRAWING NUMBER MD-522-8110-EG-CV-LAD-0102		REV C01