


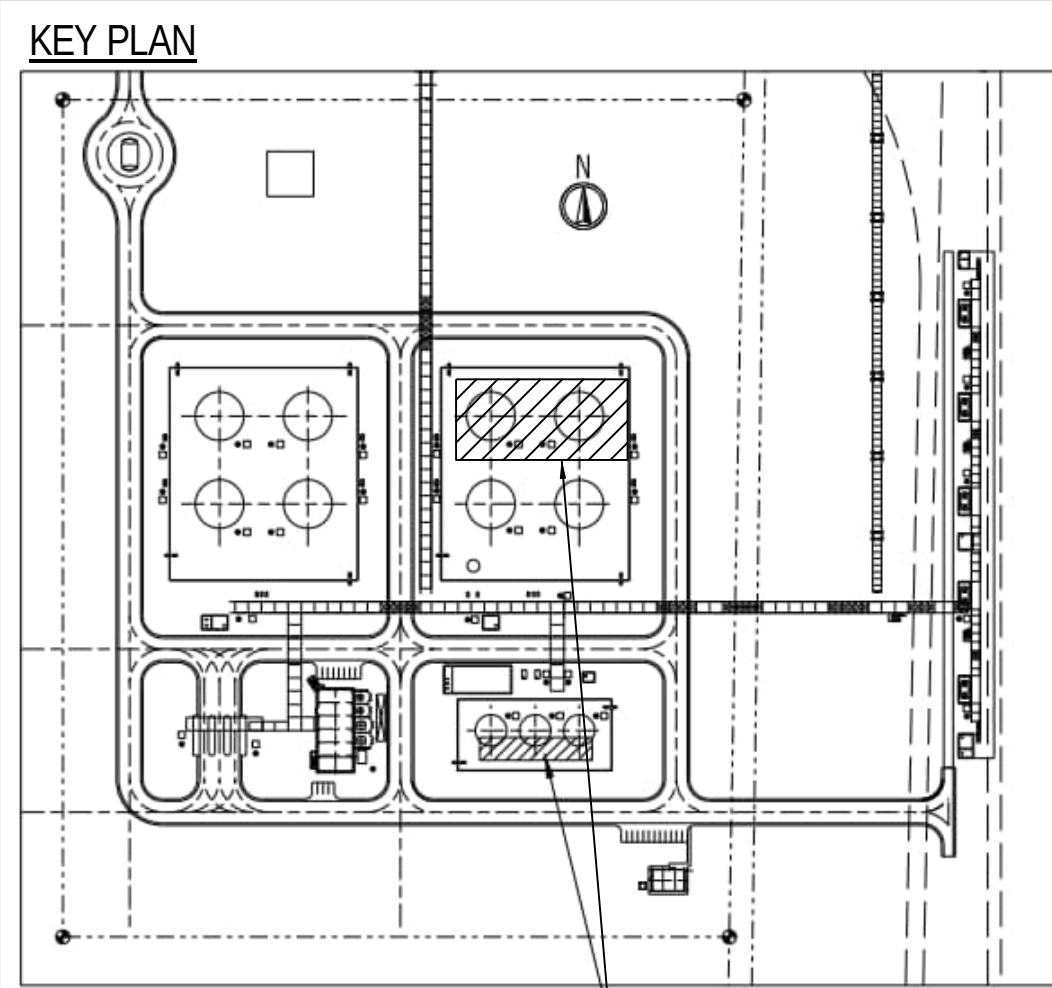

- NOTES:**
1. ALL DIMENSIONS ARE IN MILLIMETERS (MILS) (ELEVATIONS) AND COORDINATES ARE IN METERS (UNLESS OTHERWISE NOTED).
 2. FOR REFERENCE SEE: DWD NO. 522-101 (EGG-ULD 101).
 3. ALL COORDINATES ARE BASED ON THE COORDINATE SYSTEM:
FOR A GENERAL COORDINATE SYSTEM REFER DWD NO. 520-100 (EGG-ULD 100).
 4. PLANT ELEVATION: 10,000,000 msl. (COMPANY REFERENCE TO MEAN SEA LEVEL).
 5. THE MINIMUM ALLOWED TENSILE STRENGTH OF 15 MM DIA. BARS FOR CONCRETE SPECIFICATION FOR CONCRETE CONSTRUCTION.
 6. THE TYPE OF CEMENT MUST FOLLOW THE DEFINITION IN THE GEO TECHNICAL REPORT.
 7. ALL CONCRETE SHALL BE OF THE FOLLOWING TYPE:
A. CONCRETE MIX SHALL HAVE MINIMUM CHARACTERISTIC COMPRESSIVE STRENGTH OF 25 MPa.
B. CONCRETE SHALL BE INSTALLED IN ACCORDANCE WITH THE FOLLOWING:
1. FINISH-CURBED GRADE SHALL BE FINISHED CONFORMING TO ASTM A615.
2. FOR ANY CATCHES WITH LOGS SERVICES, REVERT TO DESIGN SPECIFICATION.
3. THE TYPE OF REINFORCING SHALL BE AS SPECIFIED IN DWD NO. 713.
8. ROUGHEN THE SURFACE OF THE EXISTING CONCRETE TO BLOW THE SURFACE CLEAN. THE SURFACE SHALL BE DRY AND FREE OF GREASE.
9. THE TYPE OF CEMENT SHALL BE AS SPECIFIED IN DWD NO. 713.
10. POUR NEW CONCRETE AS PER CONCRETE WORK SPECIFICATION.

LEGEND


NIL

		M/aden Phosphate 3 – Phase 1	
NAME	TITLE		SIGN
			DATE
REVIEW GRADE			
Result	Code	Description	
☐	A	Accepted	
☐	C	Proceed with exceptions to next Submission and Revision	
☐	R	Do Not Proceed - Review as noted and Resubmit	
Acceptance in any of these categories in no way relieves the Contractor/Supplier of its responsibility for the due and proper performance of the Works in accordance with the Contract/Purchase Order.			
PROJECT MANAGER SIGN-OFF:			
NAME		DATE	


ISSUED FOR CONSTRUCTION

ALL DIMENSIONS AND ELEVATIONS SHALL BE VERIFIED BEFORE STARTING THE CONSTRUCTION, ANY DISCREPANCIES SHALL BE NOTIFIED TO DESIGN TEAM.

MD-522-8110-EG-CV-LAD-0105	EXISTING MGA FOUNDATION LAYOUT PIPE SUPPORT SHT 4	Civil
MD-522-8110-EG-CV-LAD-0101	EXISTING MGA FOUNDATION LAYOUT	Civil
DRG. NO.	TITLE	REMARKS
REFERENCE DRAWINGS		
18/07/25	MA'ADEN PHOSPHATE 3 PHASE 1 RAK-RAS AL KHAIR-AREA 'A' EXISTING MGA FOUNDATION LAYOUT SH-3 PIPE SUPPORT	
18/07/25		
18/07/25		
18/07/25		
A0	DRAWING NUMBER MD-522-8110-EG-CV-LAD-0104	REV. CO.

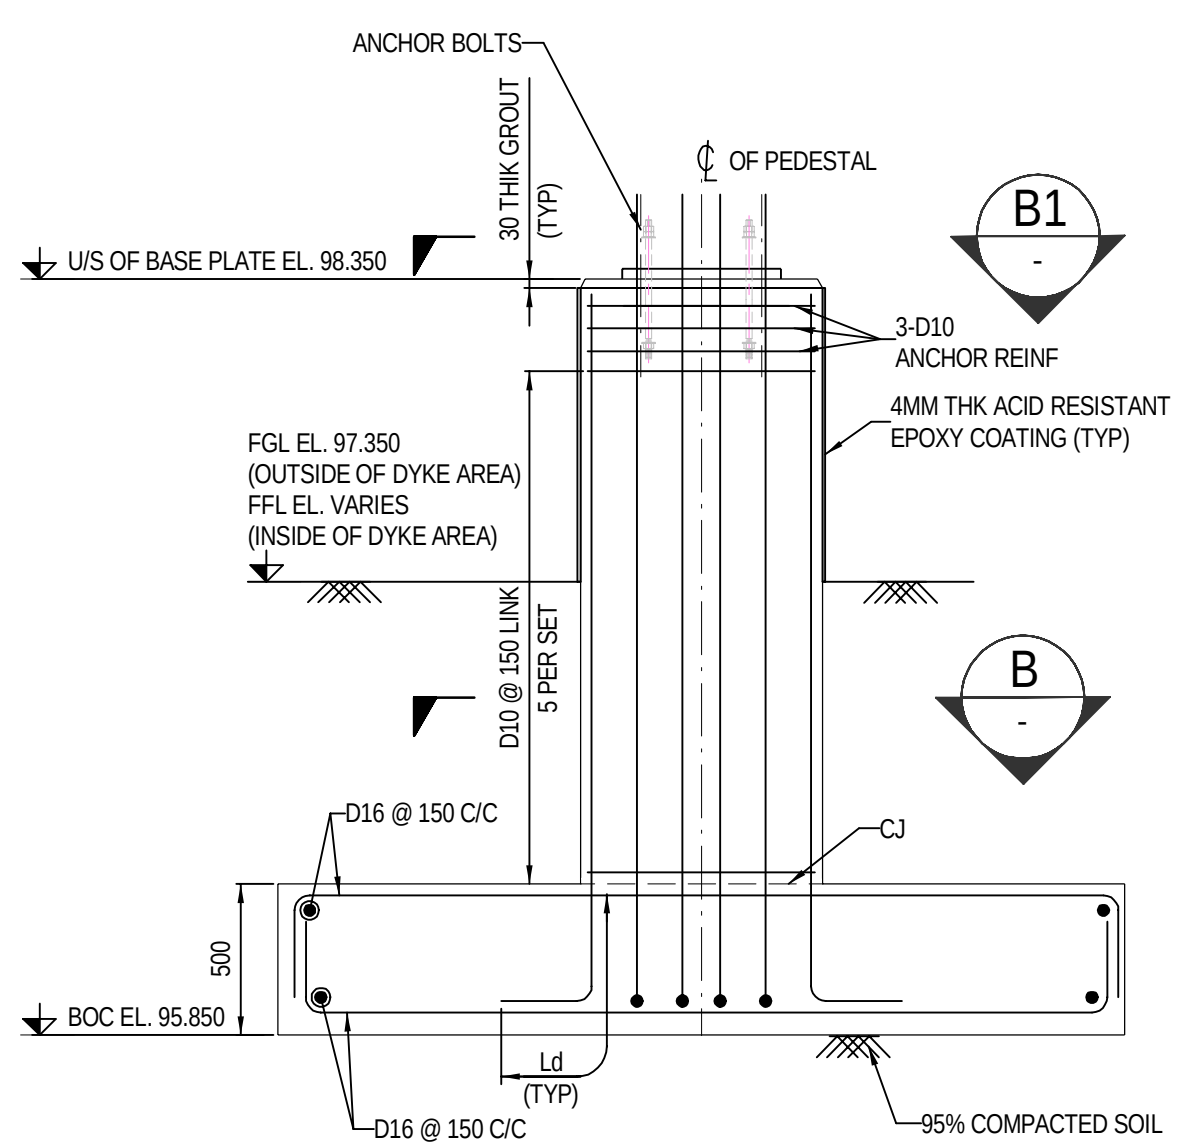


SECTION A-A
LOOKING WEST
(SCALE: 1:25 mm)

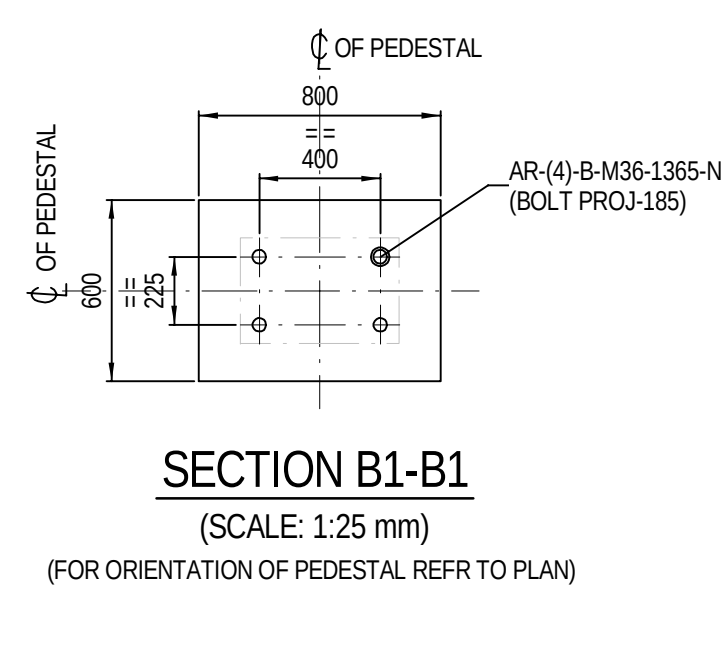


SECTION B1-B3
(SCALE: 1:25 mm)
LOCATION OF PEDESTAL REE


(FOR ORIENTATION OF PEDESTAL RECEPTOR)

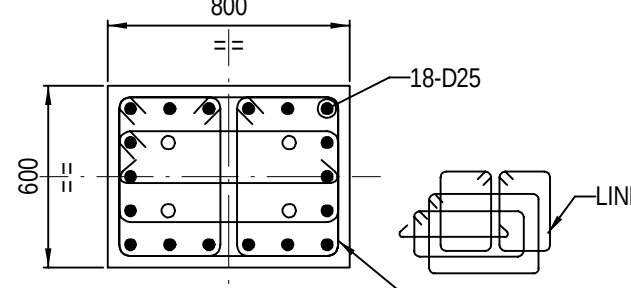

SECTION B-B
(SCALE: 1:25 mm)

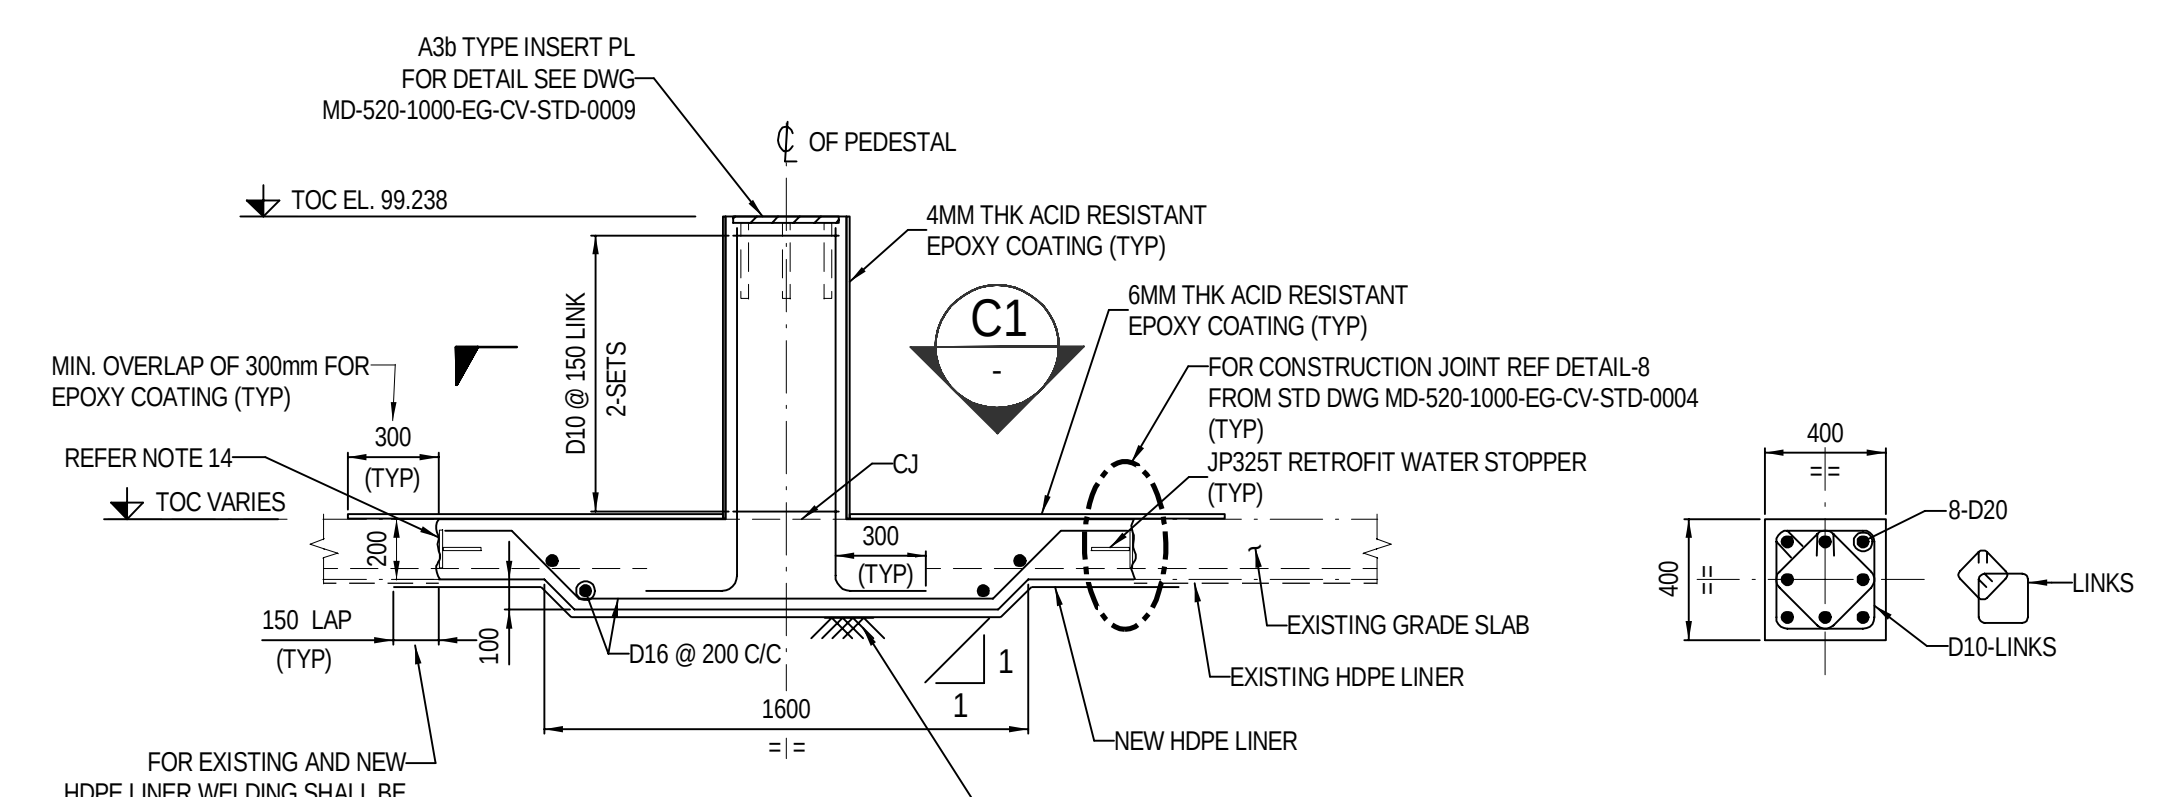

SECTION C-C
(SCALE: 1:25 mm)

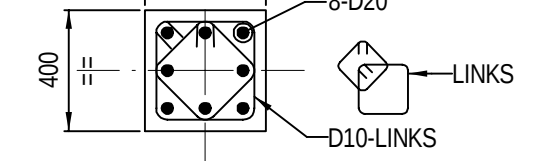

SECTION C1-C1
(SCALE: 1:25 mm)

PROPRIETARY & CONFIDENTIAL

This document and the information contained herein is Ma'aden's proprietary know-how. This document or any part thereof should not be reproduced, stored in a retrieval system or transmitted by any means, electronic or otherwise, or divulged without prior written permission of Ma'aden.

"Contractor Insignia to be placed here if applicable"



DRAWN	P.PARDULE	18/07/25
CHECKED	A.KAMTEKAR	18/07/25
ENGINEER	V.SHINDE	18/07/25
APPROVED	V.DHAPATKAR	18/07/25
EMPLOYER	MA'ADEN	
SCALE	1:1	A0

[illegible]