


DRAWING NUMBER MD-522-8110-EG-CV-LAD-0106 REV C01

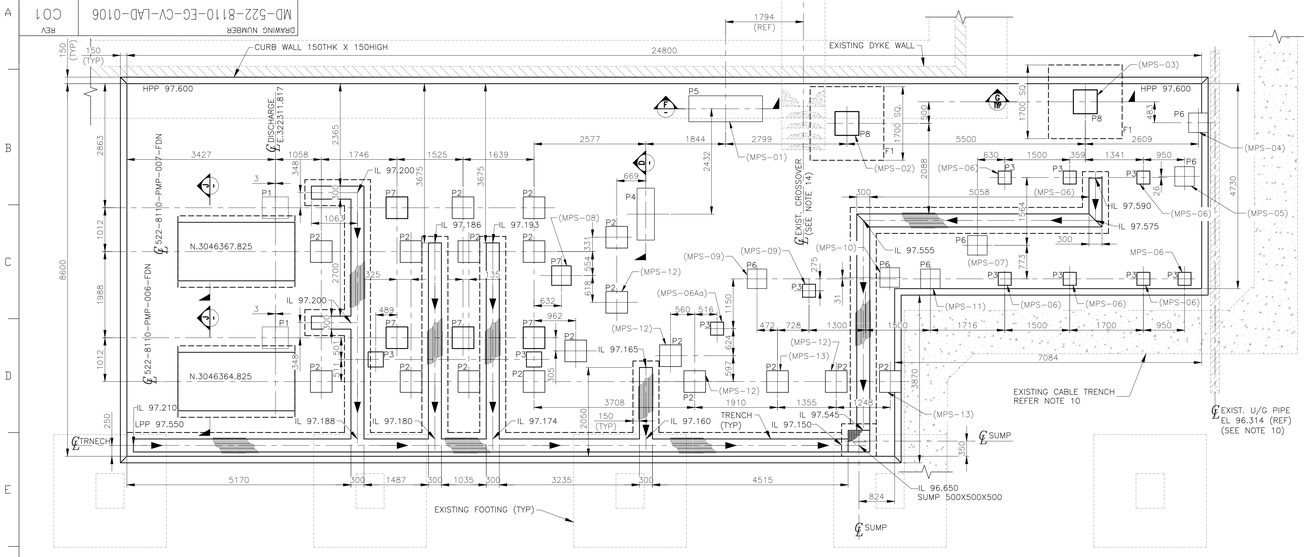


FOUNDATION LAYOUT FOR EXISTING MGA PUMP AREA GRADE SLAB & PIPE SUPPORT (TOC EL. 97.550 UNO)
(300 THK)(UNO)
Scale:1/50

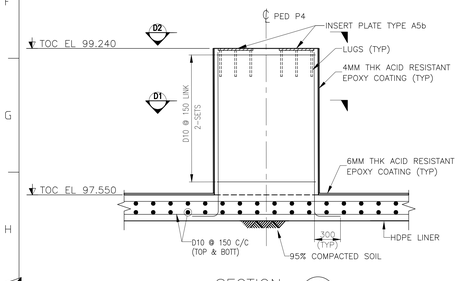

SECTION D — Scale:1/25

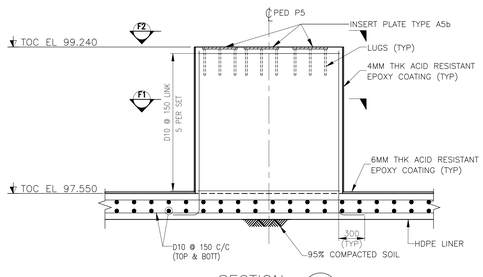


SECTION F — Scale:1/25

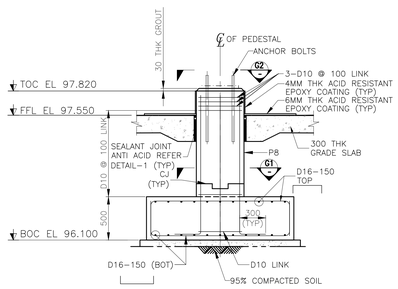


TYP DETAIL OF FOUNDATION F1


SECTION G — Scale:1/25

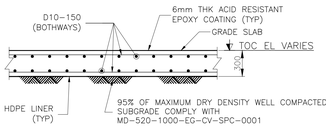


TYPICAL SECTION OF CONCRETE GRADE SLAB
Scale:1/25

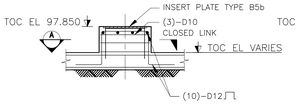


TYP DETAIL OF PEDESTAL P1(600x500) 2Nos
Scale:1/25

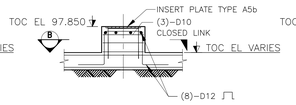


TYP DETAIL OF PEDESTAL P2(500x500) 18Nos
Scale:1/25

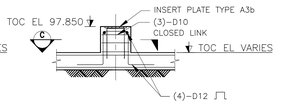


TYP DETAIL OF PEDESTAL P3(350x350) 11Nos
Scale:1/25

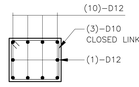


SECTION A — Scale:1/25

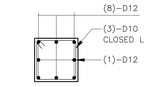


SECTION B — Scale:1/25

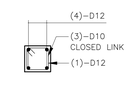


SECTION C — Scale:1/25

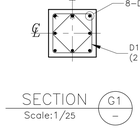


SECTION G1 — Scale:1/25

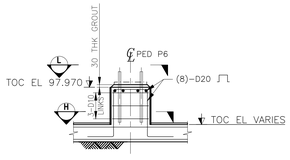


TYP DETAIL OF PEDESTAL P6(450x450) 6Nos
Scale:1/25

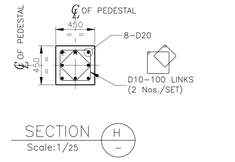


SECTION H — Scale:1/25

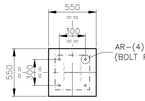


SECTION G2 — Scale:1/25

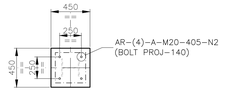


SECTION L — Scale:1/25

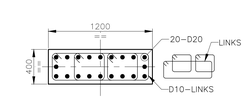


SECTION D1 — Scale:1/25

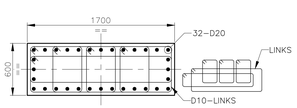

SECTION F1 — Scale:1/25

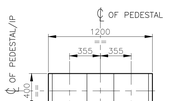


SECTION D2 — Scale:1/25

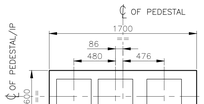


SECTION F2 — Scale:1/25




TYPICAL DETAIL OF PEDESTAL P7(500x500) 4Nos
Scale:1/25

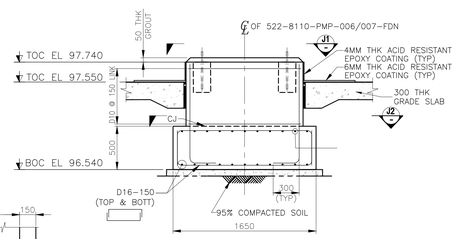


SECTION J — Scale:1/25

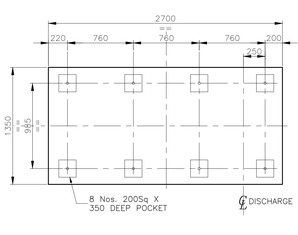


SECTION J1 — Scale:1/25

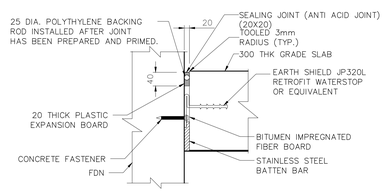


DETAIL 1 — SCALE NTS

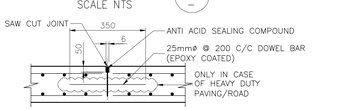


TYPICAL DETAIL OF CONTRACTION JOINT
SCALE : NTS

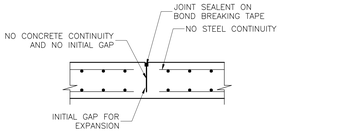


TYPICAL DETAIL OF FORMED CONRTACTION JOINT
SCALE : NTS

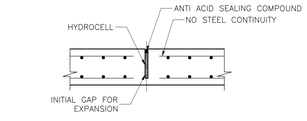


TYPICAL DETAIL OF EXPANSION JOINT
SCALE : NTS

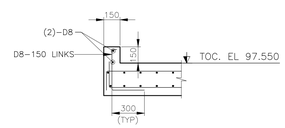


TYPICAL CURB REINFORCEMENT
Scale:1/20

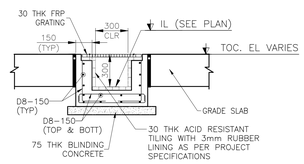

TYPICAL TRENCH REINFORCEMENT
Scale:1/20

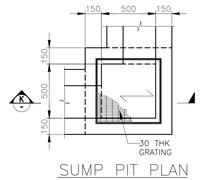


SUMP PIT PLAN
Scale:1/20

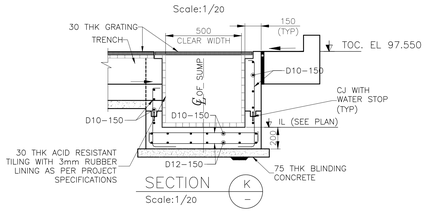


SECTION K — Scale:1/20

TYPICAL RC DETAIL OF SUMP PIT

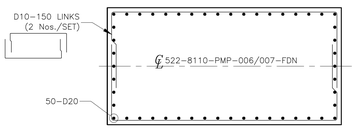

SECTION J2 — Scale:1/25

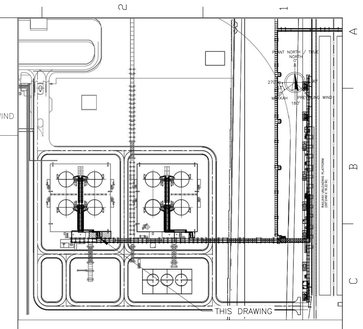

KEY PLAN:

GENERAL NOTES:

1) ALL DIMENSIONS ARE IN MILLIMETERS UNLESS OTHERWISE SPECIFIED.
2) ALL CO-ORDINATES ARE BASED ON UTM 39R COORDINATE SYSTEM.
3) ALL CO-ORDINATES AND LEVELS ARE IN METER UNLESS OTHERWISE SPECIFIED.
4) FOR GENERAL CONCRETE NOTES REFER DWG. No. MD-520-1000-EG-CV-STD-0001.
5) PLANT ELEVATION EL. 100.000 = 7.00M M.S.L (COMPANY REFERENCE TO MEAN SEA LEVEL).
6) THE TYPE OF CEMENT MUST FOLLOW THE DEFINITION IN THE GEOTECHNICAL REPORT.
7) FOR ANY CLASHES WITH U/G SERVICES, REVERT TO DESIGN OFFICE.
8) FOR BITUMINOUS COATING CONCRETE PROTECTION BELOW GROUND REFER DETAIL-15 FROM DWG. NO. MD-520-1000-EG-CV-STD-0002.
9) FOR INSERT PLATE DETAILS REFER TO DRAWINGS NO. MD-520-1000-EG-CV-STD-0009 TO 0011.
10) CONTRACTOR SHALL PROVIDE PROPER TEMPORARY SUPPORTING FOR EXISTING FACILITIES AND ADJACENT FOUNDATION DURING EXCAVATION.
11) CONSTRUCTION JOINT MAY BE PROVIDED TO SUIT AT SITE REQUIREMENTS, IN CASE PANEL SIZE IS LESS THAN THE REQUIREMENT OF EXPANSION JOINT.
12) EXPANSIONS JOINTS SHALL BE PROVIDED AS PER ACI 330R & STD DWG NO. MD-520-1000-EG-CV-STD-0004.
13) CONSTRUCTION TRANSVERSE JOINT & LONGITUDINAL JOINT SHALL BE SPACED & DETAILED FOR DOWEL AS PER ACI 224.3R.
14) 6mm THK EPOXY COATING SHALL BE APPLIED FOR FIRST TWO STEPS OF EXISTING CONCRETE STAIR (CROSSOVER).

HOLD LIST:
NIL

ISSUED FOR CONSTRUCTION

MAADEN	Maaden Phosphate 3 – Phase 1		
NAME	TITLE	SIGN	DATE

REVIEW GRADE		
Result	Code	Description
☐	A	Accepted
☐	C	Proceed with exceptions to next Submission and Revision
☐	R	Do Not Proceed - Revise as noted and Resubmit

Acceptance in any of these categories in no way relieves the Contractor/Supplier of its responsibility for the due and proper performance of the Works in accordance with the Contract/Purchase Order.

PROJECT MANAGER SIGN-OFF:			
NAME		DATE	

REFERENCES DRAWINGS:

CWP-7113-CV-CX-001 EWP-7113-CV-CX-001		
DRG. NO.	TITLE	REMARK
MD-522-8110-EG-ST-LAD-0006	EXIXTING MGA PUMP AREA PIPE SUPPORT	CIVIL

REV	DATE	REVISION DESCRIPTION	DRN	CHK	ENG	APP	EMP
C01	12/03/25	ISSUED FOR CONSTRUCTION	PP	AK	VS	VD	MAADEN
A01	12/01/25	ISSUED FOR REVIEW (IFR)	PP	AK	VS	VD	MAADEN

DOCUMENT NUMBER | REFERENCE DOCUMENTS

PROPRIETARY & CONFIDENTIAL
This document and the information contained herein is Maaden proprietary know-how. This document or any part thereof should not be reproduced, stored in a retrieval system or transmitted by any means, electronic or otherwise, or divulged without prior written permission of Maaden.

"Contractor Insignia to be placed here if applicable"

worley DELIVERING SUSTAINABLE CHANCE | JESA INTERNATIONAL | MAADEN

DRAWN	P.PARDULE	09/25/25
CHECKED	A.KAMTEKAR	09/25/25
ENGINEER	V.SHINDE	09/25/25
APPROVED	V.DHAPATKAR	09/25/25
EMPLOYER	MAADEN	–
SCALE AS SHOWN	CWA 7113	A0

MAADEN PHOSPHATE 3 PHASE 1
RAK-RAS AL KHAIR-AREA 'A'
EXISTING MGA PUMP AREA GRADE SLAB LAYOUT & PIPE SUPPORT DETAILS

DRAWING NUMBER MD-522-8110-EG-CV-LAD-0106 REV C01