

DRAWING NUMBER MD-522-8110-EG-CV-LAD-0107 REV C01

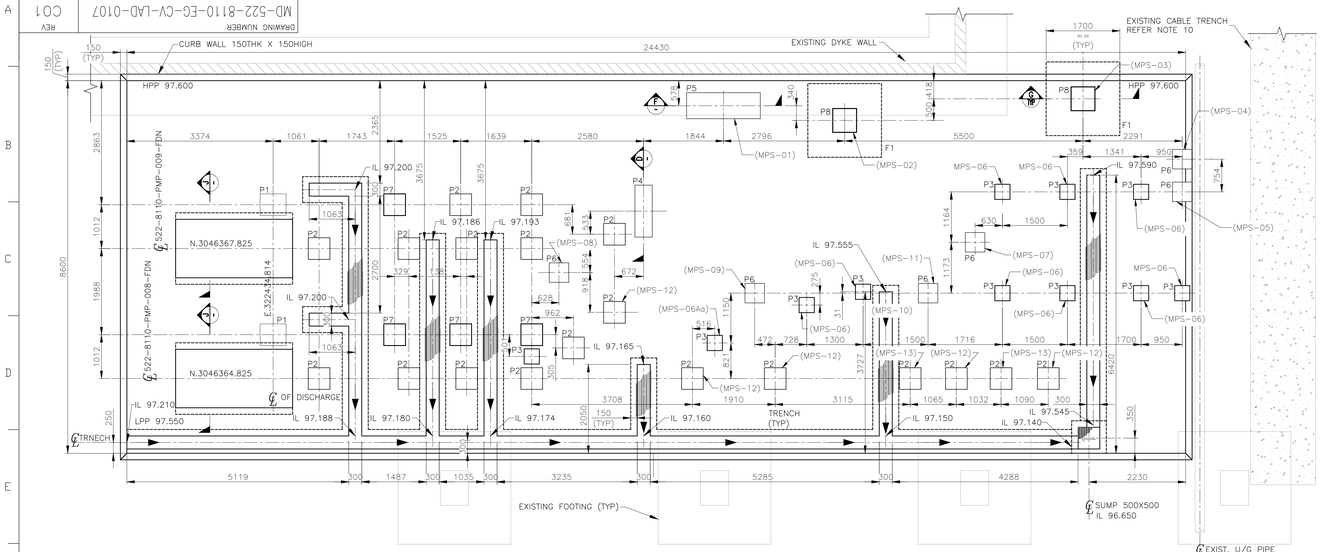


FOUNDATION LAYOUT FOR EXISTING MGA PUMP AREA GRADE SLAB & PIPE SUPPORT (TOC EL. 97.550 UNO)


(300 THK)(UNO)
Scale:1/50

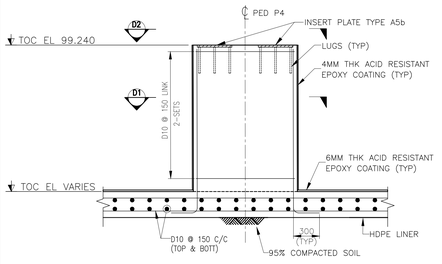

SECTION D Scale:1/25

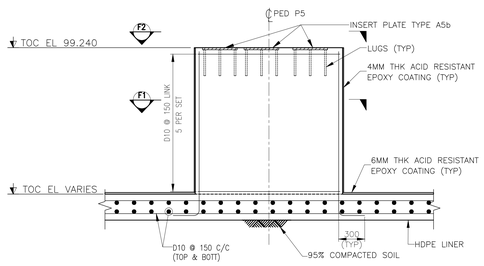


SECTION F Scale:1/25

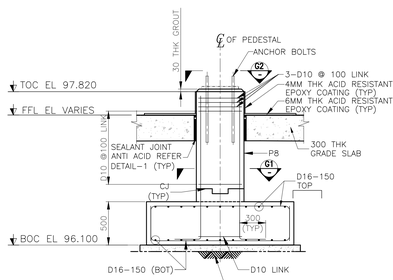


TYP DETAIL OF FOUNDATION F1

SECTION G Scale:1/25

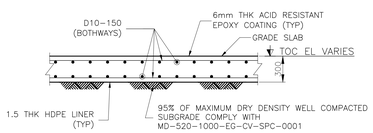

TYPICAL SECTION OF CONCRETE GRADE SLAB


Scale:1/25

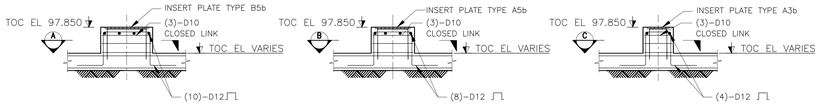


TYP DETAIL OF PEDESTAL P1(600x500) 2Nos
Scale:1/25

TYP DETAIL OF PEDESTAL P2(500x500) 20Nos
Scale:1/25


TYP DETAIL OF PEDESTAL P3(350x350) 11Nos
Scale:1/25

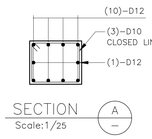


SECTION A Scale:1/25

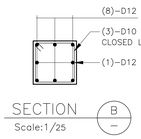


SECTION B Scale:1/25

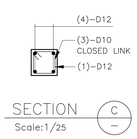


SECTION C Scale:1/25

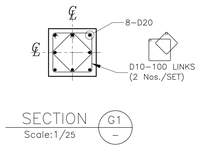


SECTION G1 Scale:1/25

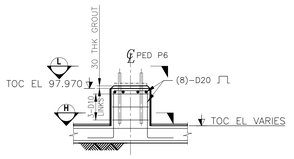


TYP DETAIL OF PEDESTAL P6(450x450) 6Nos
Scale:1/25

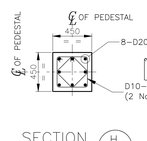


SECTION H Scale:1/25

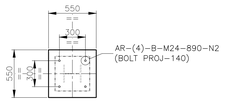


SECTION G2 Scale:1/25

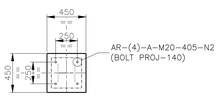


SECTION L Scale:1/25

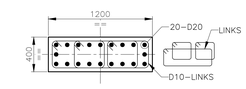


SECTION D1 Scale:1/25

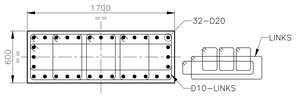


SECTION F1 Scale:1/25

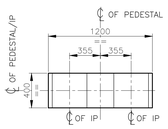


SECTION D2 Scale:1/25

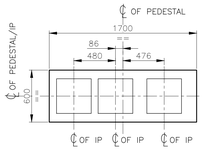


SECTION F2 Scale:1/25

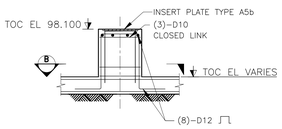


TYPICAL DETAIL OF PEDESTAL P7(500x500) 4Nos
Scale:1/25

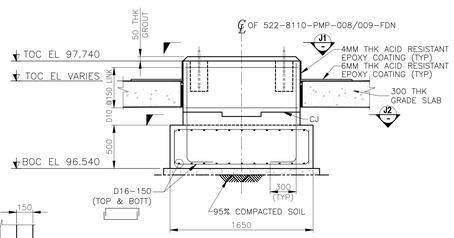


SECTION J Scale:1/25

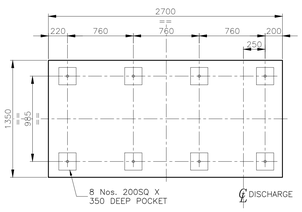


SECTION J1 Scale:1/25

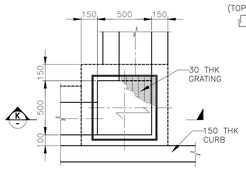


SUMP PIT PLAN
Scale:1/20

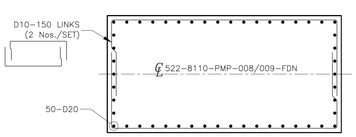


SECTION J2 Scale:1/25

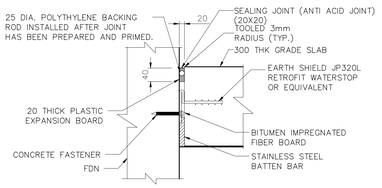


DETAIL 1 SCALE NTS

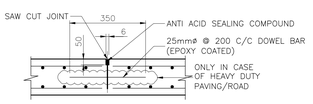


TYPICAL DETAIL OF CONTRACTION JOINT
SCALE : NTS

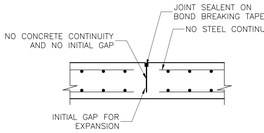


TYPICAL DETAIL OF FORMED CONRTACTION JOINT
SCALE : NTS

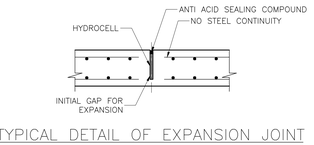


TYPICAL DETAIL OF EXPANSION JOINT
SCALE : NTS

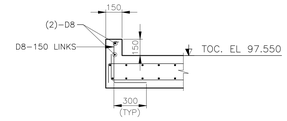

TYPICAL CURB REINFORCEMENT
Scale:1/20

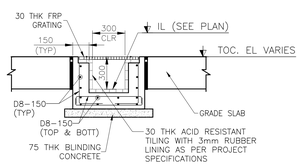



TYPICAL TRENCH REINFORCEMENT

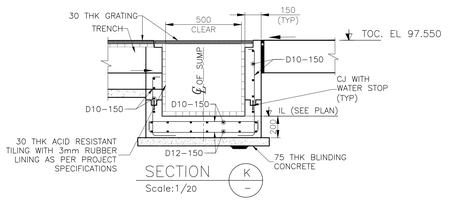

SECTION K Scale:1/20

TYPICAL RC DETAIL OF SUMP PIT

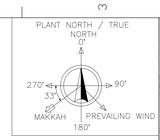

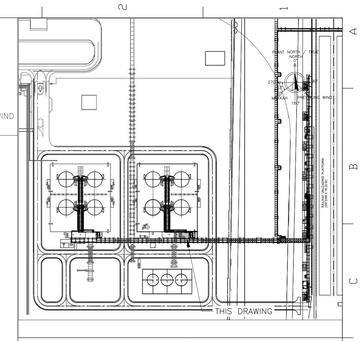

KEY PLAN:

GENERAL NOTES:

1) ALL DIMENSIONS ARE IN MILLIMETERS UNLESS OTHERWISE SPECIFIED.
2) ALL CO-ORDINATES ARE BASED ON UTM 39R COORDINATE SYSTEM.
3) ALL CO-ORDINATES AND LEVELS ARE IN METER UNLESS OTHERWISE SPECIFIED.
4) FOR GENERAL CONCRETE NOTES REFER DWG. No. MD-520-1000-EG-CV-STD-0001.
5) PLANT ELEVATION EL. 100.000 = 7.00M M.S.L (COMPANY REFERENCE TO MEAN SEA LEVEL).
6) THE TYPE OF CEMENT MUST FOLLOW THE DEFINITION IN THE GEOTECHNICAL REPORT.
7) FOR ANY CLASHES WITH U/G SERVICES, REVERT TO DESIGN OFFICE.
8) FOR BITUMINOUS COATING CONCRETE PROTECTION BELOW GROUND REFER DETAIL-15 FROM DWG. NO. MD-520-1000-EG-CV-STD-0002.
9) FOR INSERT PLATE DETAILS REFER TO DRAWINGS NO. MD-520-1000-EG-CV-STD-0009 TO 0011.
10) CONTRACTOR SHALL PROVIDE PROPER TEMPORARY SUPPORTING FOR EXISTING FACILITIES AND ADJACENT FOUNDATION DURING EXCAVATION.
11) CONSTRUCTION JOINT MAY BE PROVIDED TO SUIT AT SITE REQUIREMENTS, IN CASE PANEL SIZE IS LESS THAN THE REQUIREMENT OF EXPANSION JOINT.
12) EXPANSIONS JOINTS SHALL BE PROVIDED AS PER ACI 330R & STD DWG NO. MD-520-1000-EG-CV-STD-0004.
13) CONSTRUCTION TRANSVERSE JOINT & LONGITUDINAL JOINT SHALL BE SPACED & DETAILED FOR DOWEL AS PER ACI 224.3R.

HOLD LIST:

NIL

ISSUED FOR CONSTRUCTION

MAADEN	Maaden Phosphate 3 – Phase 1		
NAME	TITLE	SIGN	DATE

REVIEW GRADE		
Result	Code	Description
☐	A	Accepted
☐	C	Proceed with exceptions to next Submission and Revision
☐	R	Do Not Proceed - Revise as noted and Resubmit

Acceptance in any of these categories in no way relieves the Contractor/Supplier of its responsibility for the due and proper performance of the Works in accordance with the Contract/Purchase Order.

PROJECT MANAGER SIGN-OFF:			
NAME		DATE	

REFERENCES DRAWINGS:

DRG. NO.	TITLE	REMARK
MD-522-8110-EG-ST-LAD-0009	EXIXTING MGA PUMP AREA PIPE SUPPORT	CIVIL
CWP-7113-CV-CX-001		
EWP-7113-CV-CX-001		

REV	DATE	REVISION DESCRIPTION	DRN	CHK	ENG	APP	EMP
C01	12/05/25	ISSUED FOR CONSTRUCTION (IFC)	PP	AK	VS	VD	MAADEN
A01	30/09/25	ISSUED FOR REVIEW (IFR)	PP	AK	VS	VD	MAADEN

DOCUMENT NUMBER | REFERENCE DOCUMENTS

PROPRIETARY & CONFIDENTIAL
This document and the information contained herein is Ma'aden proprietary know-how. This document or any part thereof should not be reproduced, stored in a retrieval system or transmitted by any means, electronic or otherwise, or divulged without prior written permission of Ma'aden.

"Contractor Insignia to be placed here if applicable"

worley DELIVERING SUSTAINABLE CHANGE | JESA INTERNATIONAL | MAADEN

DRAWN	P.PARDULE	30/09/25	
CHECKED	A.KAMTEKAR	30/09/25	
ENGINEER	V.SHINDE	30/09/25	
APPROVED	V.DHAPATKAR	30/09/25	
EMPLOYER	MAADEN	–	
SCALE AS SHOWN	CWA 7113	A0	

MAADEN PHOSPHATE 3 PHASE 1
RAK-RAS AL KHAIR-AREA 'A'
EXISTING MGA PUMP AREA GRADE SLAB LAYOUT & PIPE SUPPORT DETAILS

DRAWING NUMBER MD-522-8110-EG-CV-LAD-0107 REV C01