

DRAWING NUMBER MD-522-8110-EG-CV-LAD-0115 | REV C01

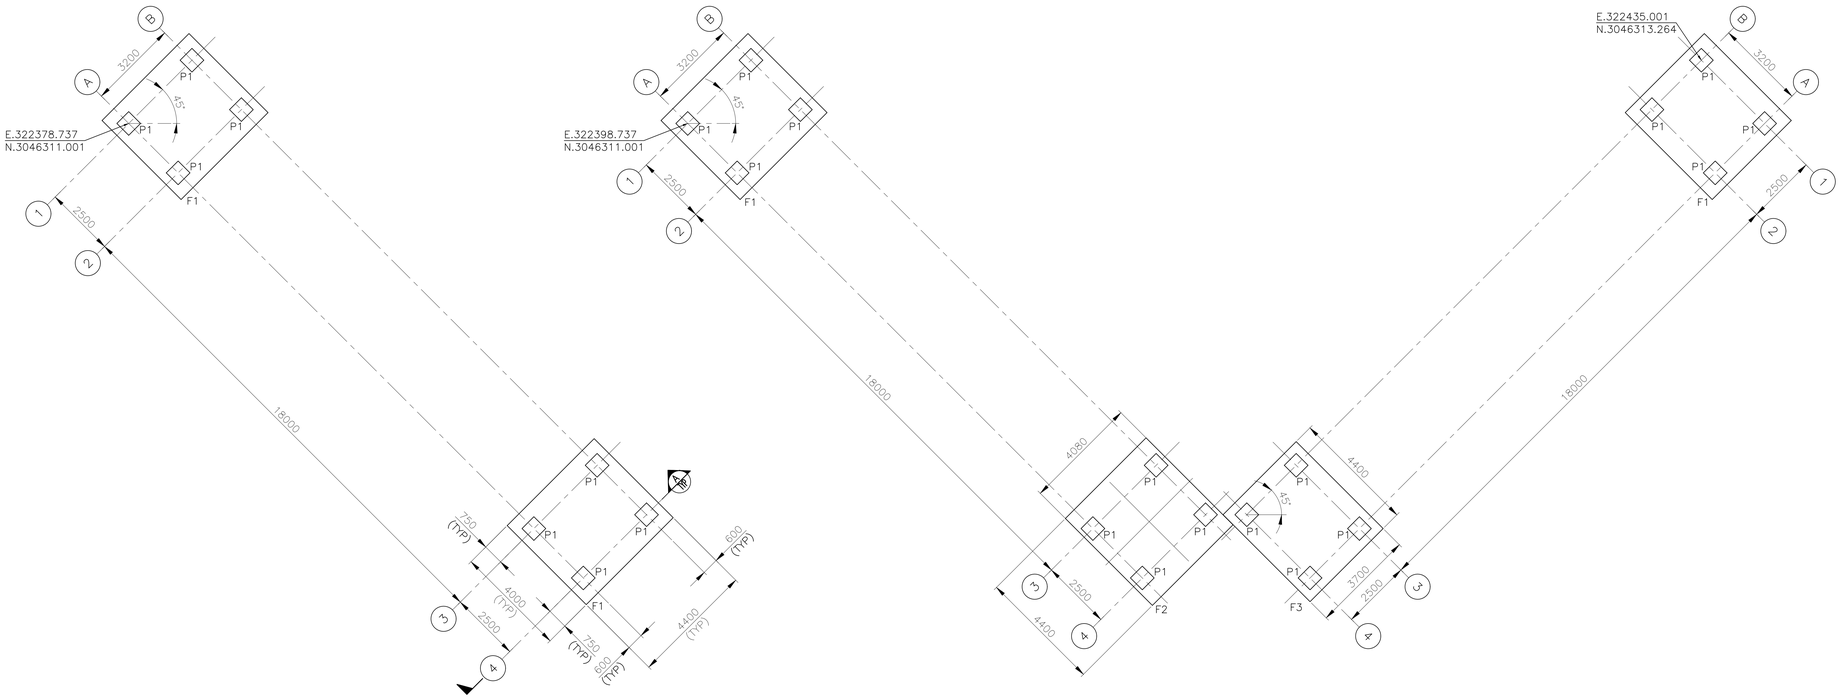


FOUNDATION LAYOUT FOR AGITATOR PLATFORM STRUCTURES

Scale:1/75

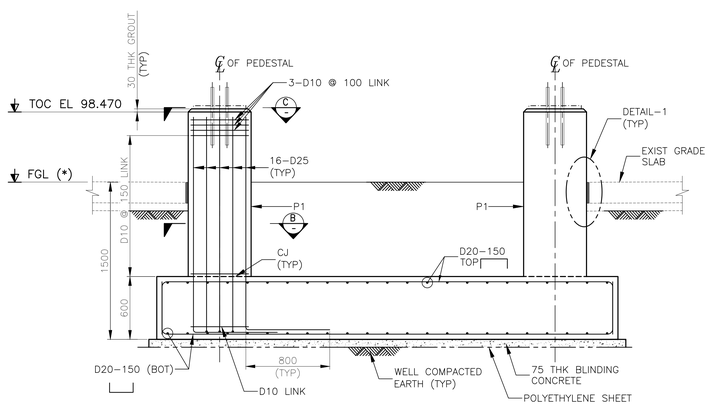


SECTION A
Scale:1/20


(FOR FOOTING NO. AND SIZE REFER PLAN)
('*'– FGL SHOULD BE FOLLOWED AS PER SITE CONDITION, BOTTOM OF FOOTING MINIMUM 1.5M BELOW FGL)

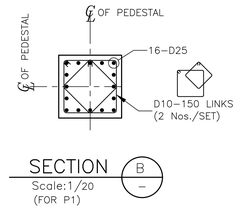


SECTION B
Scale:1/20
(FOR P1)

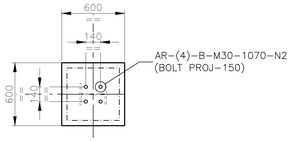

SECTION C
Scale:1/20
(FOR P1)

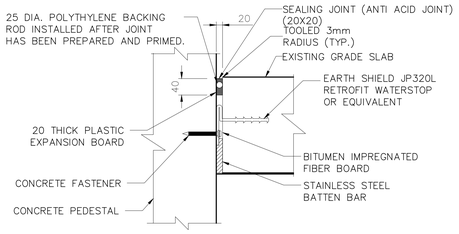

DETAIL 1
SCALE NTS

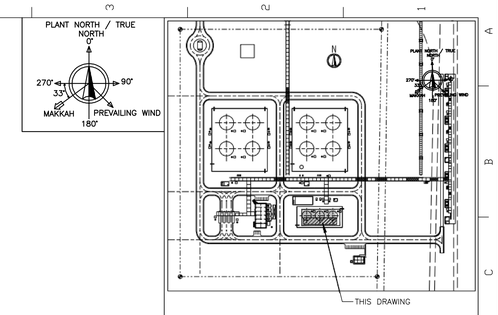

KEY PLAN:

GENERAL NOTES:

1) ALL DIMENSIONS ARE IN MILLIMETERS UNLESS OTHERWISE SPECIFIED.
2) ALL CO–ORDINATES ARE BASED ON UTM 39R COORDINATE SYSTEM.
3) ALL CO–ORDINATES AND LEVELS ARE IN METER UNLESS OTHERWISE SPECIFIED.
4) FOR GENERAL CONCRETE NOTES REFER DWG. No. MD–520–1000–EG–CV–STD–0001.
5) PLANT ELEVATION EL. 100.000 = 7.00M M.S.L (COMPANY REFERENCE TO MEAN SEA LEVEL).
6) THE TYPE OF CEMENT MUST FOLLOW THE DEFINITION IN THE GEOTECHNICAL REPORT.
7) FOR ANY CLASHES WITH U/G SERVICES, REVERT TO DESIGN OFFICE.
8) FOR BITUMINOUS COATING CONCRETE PROTECTION BELOW GROUND REFER DETAIL–15 FROM DWG. NO. MD–520–1000–EG–CV–STD–0002.

HOLD LIST:

NIL

Ma'aden Phosphate 3 – Phase 1			
NAME	TITLE	SIGN	DATE

REVIEW GRADE

Result	Code	Description
☐	A	Accepted
☐	C	Proceed with exceptions to next Submission and Revision
☐	R	Do Not Proceed - Revise as noted and Resubmit

Acceptance in any of these categories in no way relieves the Contractor/Supplier of its responsibility for the due and properperformance of the Works in accordance with the Contract/Purchase Order.

PROJECT MANAGER SIGN-OFF:

NAME		DATE	

ISSUED FOR CONSTRUCTION

REFERENCES DRAWINGS:

DRG. NO.	TITLE	REMARK
MD–522–8110–EG–ST–LAD–0017	AGITATOR SUPPORTING STRUCTURE BASE PLATE AND PLAN VIEW (37213–AGI–503)	CIVIL
MD–522–8110–EG–ST–LAD–0015	AGITATOR SUPPORTING STRUCTURE BASE PLATE AND PLAN VIEW (37213–AGI–501/502)	CIVIL
MD–522–8000–EG–PI–PPD–0003	OVERALL PLOT PLAN	PIPING
CWP–7113–CV–CF–001		
EWP–7113–CV–CF–001		

REV	DATE	REVISION DESCRIPTION	DRN	CHK	ENG	APP	EMP
C01	27/10/25	ISSUED FOR CONSTRUCTION (IFC)	MI	AK	VS	VD	MA'ADEN
A01	22/09/25	ISSUED FOR REVIEW (IFR)	MI	AK	VS	VD	MA'ADEN

DOCUMENT NUMBER | REFERENCE DOCUMENTS

PROPRIETARY & CONFIDENTIAL
This document and the information contained herein is Ma'aden proprietary know-how. This document or any part thereof should not be reproduced, stored in a retrieval system or transmitted by any means, electronic or otherwise, or divulged without prior written permission of Ma'aden.

"Contractor Insignia to be placed here if applicable"

worley DELIVERING SUSTAINABLE CHANGE | JESA INTERNATIONAL | MA'ADEN

DRAWN	M.IJAZ	11/09/25
CHECKED	A.KAMTEKAR	11/09/25
ENGINEER	V.SHINDE	11/09/25
APPROVED	V.DHAPATKAR	11/09/25
EMPLOYER	MA'ADEN	–
SCALE	AS SHOWN	CWA 7113

MA'ADEN PHOSPHATE 3
PHASE 1 RAK – Ras Al Khair
AGITATOR PLATFORM FOUNDATION PLAN & RC DETAILS

DRAWING NUMBER MD–522–8110–EG–CV–LAD–0115 | REV C01 | A0