

DRAWING NUMBER: MD-522-8120-EG-CV-LAD-0101 | REV: C03

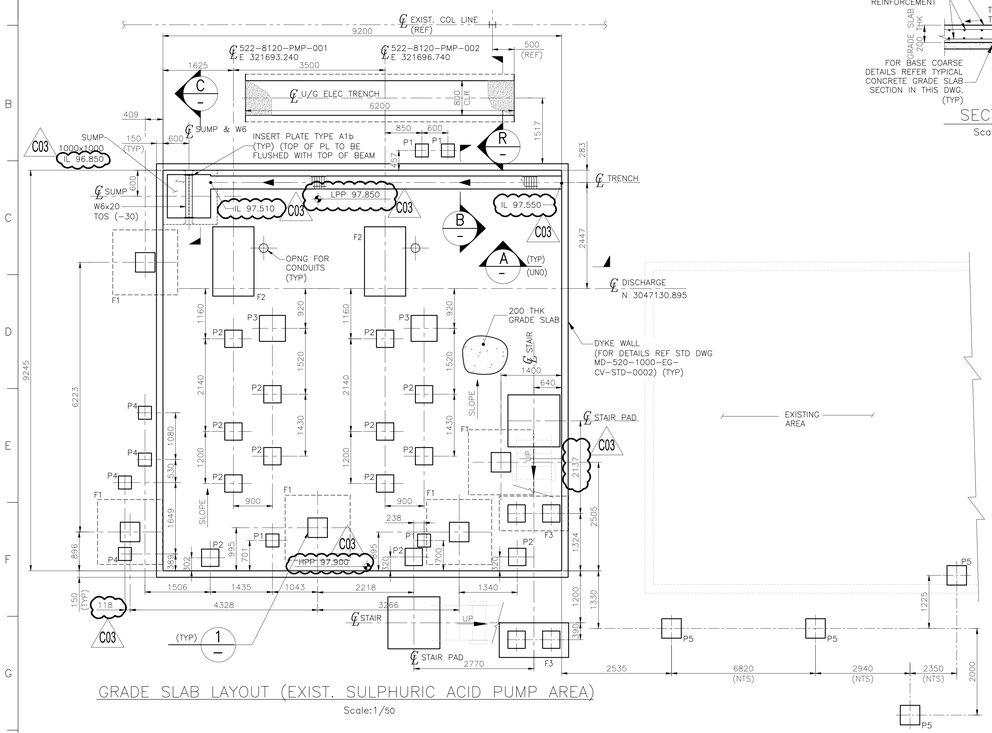


GRADE SLAB LAYOUT (EXIST. SULPHURIC ACID PUMP AREA)

Scale:1/50

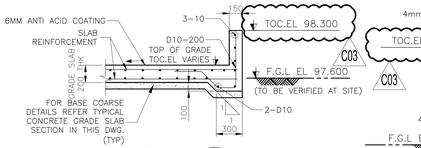


SECTION (A) Scale:1/25


DETAIL (2) SCALE: 1:25 FOR GA ONLY

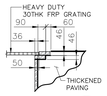


DETAIL (3) SCALE: 1:25

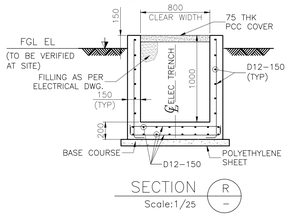

SECTION (R) Scale:1/25

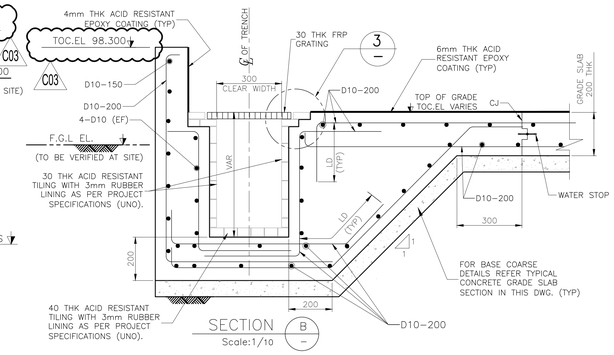


SECTION (B) Scale:1/10

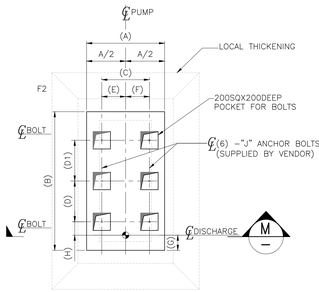


TYPICAL DETAIL OF PUMPS FOUNDATION F2


Scale:1/25

PUMP NO.	FDN NO.	TOC EL (METER)	(A) (MM)	(B) (MM)	(C) (MM)	(D) (MM)	(D1) (MM)	(E) (MM)	(F) (MM)	(G) (MM)	(H) (MM)
522-8120-PMP-001	F2	98.447	950	1600	550	470	470	275	275	175	155
522-8120-PMP-002											

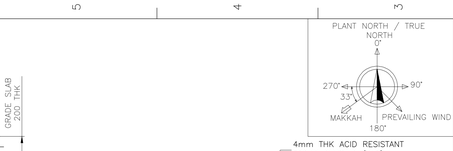


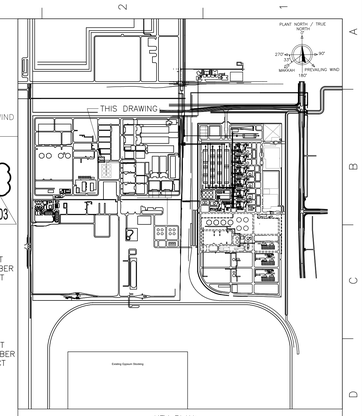

KEY PLAN:

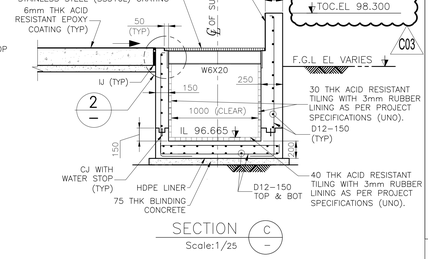

SECTION (C) Scale:1/25

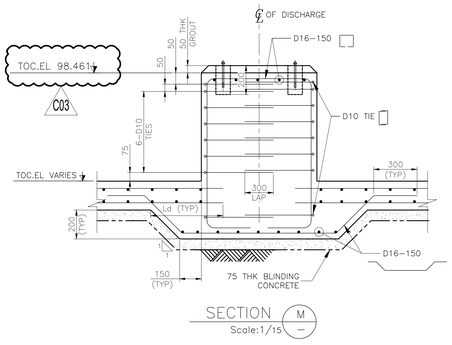

SECTION (M) Scale:1/15


GENERAL NOTES:

1) ALL DIMENSIONS ARE IN MILLIMETERS UNLESS OTHERWISE SPECIFIED.
2) ALL CO-ORDINATES ARE BASED ON UTM 39R COORDINATE SYSTEM.
3) ALL CO-ORDINATES AND LEVELS ARE IN METER UNLESS OTHERWISE SPECIFIED.
4) FOR GENERAL CONCRETE NOTES REFER DWG. No. MD-520-1000-EG-CV-STD-0001.
5) PLANT ELEVATION EL 100.000 = 7.00M M.S.L (COMPANY REFERENCE TO MEAN SEA LEVEL).
6) THE TYPE OF CEMENT MUST FOLLOW THE DEFINITION IN THE GEOTECHNICAL REPORT.
7) FOR ANY CLASHES WITH U/G SERVICES, REVERT TO DESIGN OFFICE.
8) FOR CONSTRUCTION & ISOLATION JOINTS REFER TO DWG No.MD-520-1000-EG-CV-STD-0004 (UNO).
9) ALL REBARS SHALL BE EPOXY COATED.
10) CONCRETE MIX SHALL HAVE MINIMUM CYLINDRICAL COMPRESSIVE STRENGTH OF 35 MPa FOR CAST IN SITU CONCRETE.
11) REINFORCEMENT GRADE SHALL BE 420N/mm² CONFIRMING TO ASTM A615M.
12) FOR STANDARD INSERT PLATE DETAILS, SEE DWG MD-520-1000-EG-CV-STD-0009.
13) SAW CUT JOINTS TO BE CLEANED & FILLED BY SEALING COMPOUND AFTER CURING & AS DIRECTED BY OWNER/CONSULTANT.
14) CONSTRUCTION JOINT MAY BE PROVIDED TO SUIT AT SITE REQUIREMENTS, IN CASE PANEL SIZE IS LESS THAN THE REQUIREMENT OF EXPANSION JOINT.
15) EXPANSIONS JOINTS SHALL BE PROVIDED AS PER ACI 330R & STD DWG NO. MD-520-1000-EG-CV-STD-0004.
16) CONSTRUCTION TRANSVERSE JOINT & LONGITUDINAL JOINT SHALL BE SPACED & DETAILED FOR DOWEL AS PER ACI 224.3R.
17) ALL ELEVATIONS AND DISTANCE SHALL BE CONFIRMED BY CONTRACTOR WITH TECHNICAL SERVICES TEAM BEFORE EXECUTING THE WORK, ANY DISCRIPANCY SHALL BE INFORMED TO DESIGN OFFICE.

LEGEND & ABBREVATION:


F : FOUNDATION
P : PEDESTAL
IJ : ISOLATION JOINT

HOLDS:

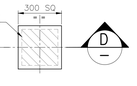


DETAIL OF PEDESTAL P1

(1 NO.) Scale:1/15

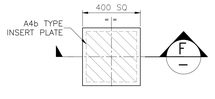


DETAIL OF PEDESTAL P2

(14 NOS) Scale:1/15

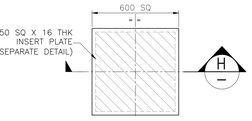


DETAIL OF PEDESTAL P3

(2 NOS) Scale:1/15

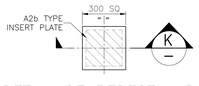


DETAIL OF PEDESTAL P4

(4 NOS) Scale:1/15

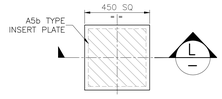


DETAIL OF PEDESTAL P5

(2 NOS) Scale:1/15

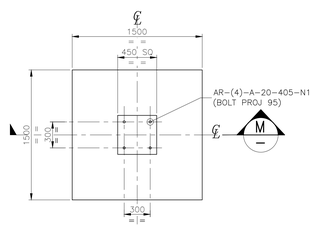


TYPICAL DETAIL OF FOUNDATION F1

Scale:1/25

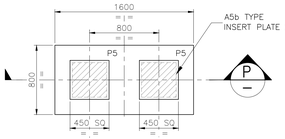


DETAIL OF FOUNDATION F3


Scale:1/25

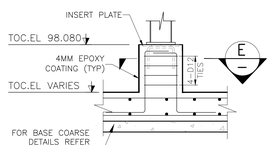


SECTION (D) Scale:1/15

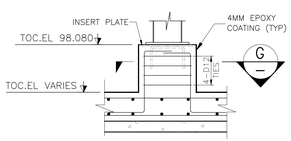


SECTION (F) Scale:1/15

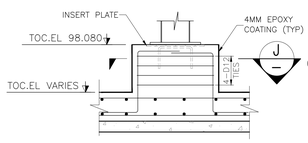


SECTION (H) Scale:1/15

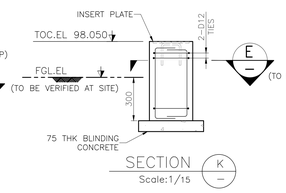


SECTION (K) Scale:1/15

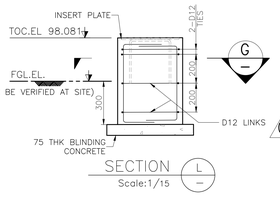

SECTION (L) Scale:1/15

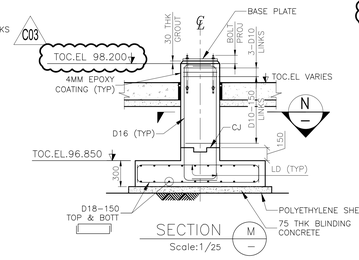


SECTION (M) Scale:1/25

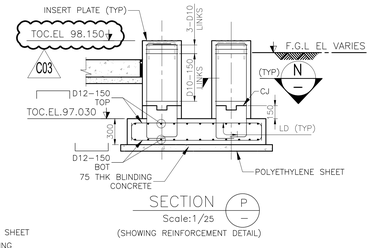


SECTION (P) Scale:1/25


(SHOWING REINFORCEMENT DETAIL)

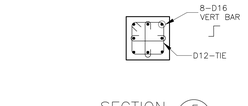


SECTION (E) Scale:1/15

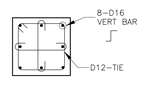

SECTION (G) Scale:1/15

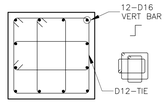


SECTION (J) Scale:1/15

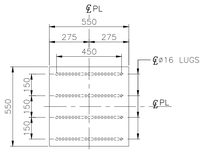


DETAIL OF INSERT PL

Scale:1/15

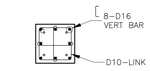


SECTION (N) Scale:1/25

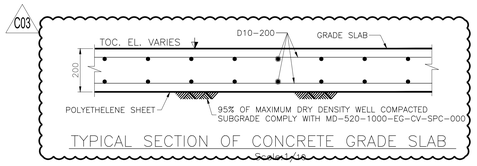


TYPICAL SECTION OF CONCRETE GRADE SLAB

Scale:1/15

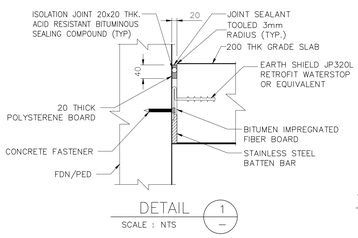


DETAIL (1) SCALE : NTS

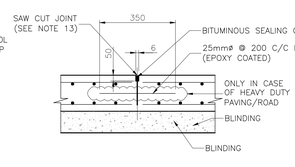


TYPICAL DETAIL OF CONTRACTION JOINT

SCALE : NTS

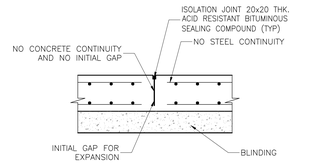


TYPICAL DETAIL OF FORMED CONRTACTION JOINT

SCALE : NTS

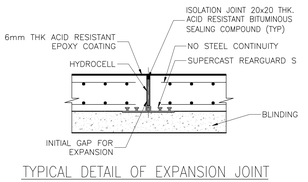

TYPICAL DETAIL OF EXPANSION JOINT

SCALE : NTS

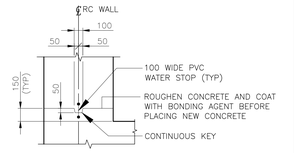

TYP DETAIL OF CONSTRUCTION JOINT CJ

SCALE: 1:25

NOTE:
REINFORCING TO BE CONTINUOUS THROUGH JOINTS

ISSUED FOR CONSTRUCTION

MAADEN	Maaden Phosphate 3 – Phase 1		
NAME	TITLE	SIGN	DATE

REVIEW GRADE		
Result	Code	Description
☐	A	Accepted
☐	C	Proceed with exceptions to next Submission and Revision
☐	R	Do Not Proceed - Revise as noted and Resubmit

Acceptance in any of these categories in no way relieves the Contractor/Supplier of its responsibility for the due and proper performance of the Works in accordance with the Contract/Purchase Order.

PROJECT MANAGER SIGN-OFF:		
NAME		DATE

CWP-0111-CV-CX-001
EWP-0111-CV-CX-001

REV	DATE	REVISION DESCRIPTION	DRN	CHK	ENG	APP	EMP
C03	12/23/25	REVISED AS MARKED – ISUUED FOR CONSTRUCTION (IFC)	S.P.	A.K.	V.S.	V.D.	MAADEN
C02	12/11/25	REVISED AS MARKED – ISSUED FOR CONSTRUCTION (IFC)	S.P.	A.K.	V.S.	V.D.	MAADEN
C01	05/21/25	ISSUED FOR CONSTRUCTION (IFC)	S.P.	A.K.	V.S.	V.D.	MAADEN
A01	04/28/25	ISSUED FOR REVIEW (IFR)	S.T.	A.K.	V.S.	V.D.	MAADEN

DOCUMENT NUMBER	REFERENCE DOCUMENTS
MD-522-1000-EG-EL-LAD-0039	CABLE TRAY LAYOUT SULPHURIC CONNECTION
MD-522-8120-EG-PI-PPD-0001	EXISTING SUPPHURIC ACID PUMPS STATION PLOT PLAN
MD-522-8120-EG-ME-GAD-ITT3-0001	SULPHURIC ACID CONCENTRATED PUMP GENERAL ARRANGMENT (MECHANICAL)

PROPRIETARY & CONFIDENTIAL

This document and the information contained herein is Maaden proprietary know-how. This document or any part thereof should not be reproduced, stored in a retrieval system or transmitted by any means, electronic or otherwise, or divulged without prior written permission of Maaden.

"Contractor insignia to be placed here if applicable"

worley DELIVERING SUSTAINABLE CHANGE | JESA INTERNATIONAL | MAADEN

DRAWN	S. TUKRUL	01/08/25	
CHECKED	A.KAMTEKAR	01/08/25	
ENGINEER	S.ELBAKOUCHI	01/08/25	
APPROVED	V.DHAPATKAR	01/08/25	
EMPLOYER	MAADEN	–	
SCALE AS NOTED	CWA 0111	A0	

MAADEN PHOSPHATE 3
PHASE 1 RAK – Ras Al Khair
EXISTING SULPHURIC ACID PUMP AREA
GRADE SLAB & FOUNDATION DETAILS

DRAWING NUMBER: MD-522-8120-EG-CV-LAD-0101 | REV: C03